NOTE: IF THIS SHEET IS NOT 30"W x 42"D, THEN IT IS NOT THE INTENDED SIZE. IN ALL CASES, WORK TO FIGURED DIMENSIONS.

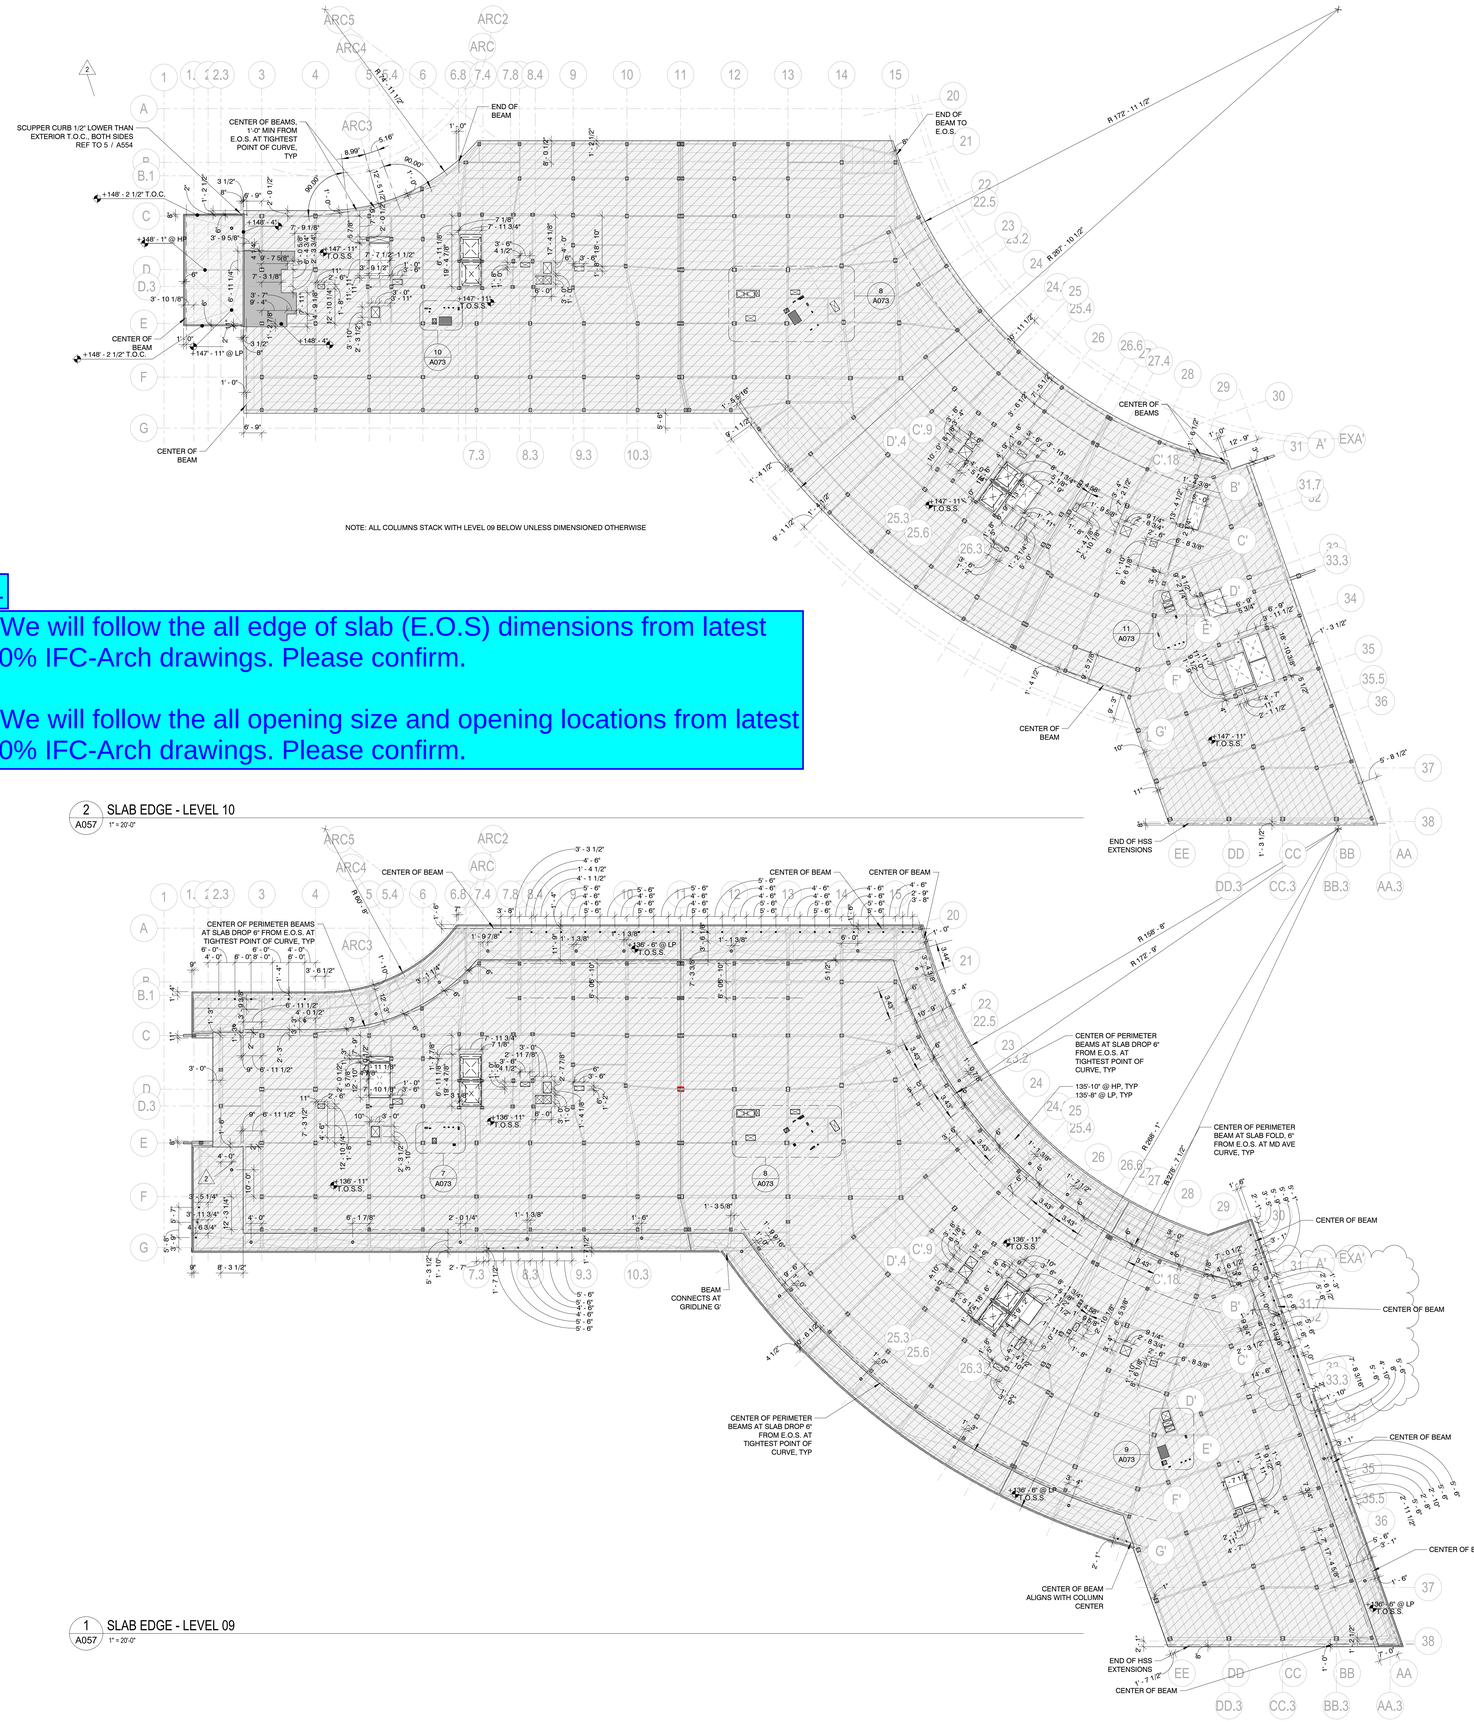

Q1

1) We will follow the all edge of slab (E.O.S) dimensions from latest 100% IFC-Arch drawings. Please confirm.

2) We will follow the all opening size and opening locations from latest 100% IFC-Arch drawings. Please confirm.

2 SLAB EDGE - LEVEL 10
A057 1" = 20'-0"

1 SLAB EDGE - LEVEL 09
A057 1" = 20'-0"

NEW FLOOR STEEL STRUCTURE NOTES:

1. SEE STRUCTURAL DRAWINGS FOR STEEL SIZING & LOCATIONS
2. NEW STEEL COLUMNS ALIGNED W/ EXISTING CONCRETE COLUMNS BELOW UNLESS NOTED OTHERWISE. DIMENSIONS PROVIDED FOR COLUMNS NOT ALIGNED W/ BELOW.
3. SEE STRUCTURAL DRAWINGS FOR STEEL COLUMN SIZING & SHAPE. RECTANGULAR GRAPHIC SHOWN IN ARCHITECTURAL PLANS ALSO REPRESENTS GYPSUM FURRING NEEDED FOR RATING.

LEGEND
- NEW STEEL COLUMN, ALIGNED WITH COLUMN BELOW
- NEW STEEL COLUMN SUPPORTED BY BEAM BELOW, SEE DIMENSIONS

SLAB EDGE DRAWING NOTES:

1. SLAB DRAWINGS ARE BASED ON ORIGINAL EXISTING DRAWINGS. ALL LOCATIONS & DIMENSIONS TO BE VERIFIED IN FIELD. CONTRACTOR TO NOTIFY ARCHITECT OF ANY OPENINGS NOT DRAWINGS. OF INFILL.
2. SEE DEMOLITI NEW OPENING DEMOLITION, & ARE TO BE CUT
3. SEE ADDITIONA DEMOLITION D ELEVATOR PITS
4. NEW INFILLS A EXTENSIONS A ADJACENT SLA NOTED OTHER
5. SEE A06# SER PERIMETER PLANS. DIMENSIONS OF PERIMETER OMMITED FROM THIS DRAWING FOR CLARITY.

LEGEND
- EXISTING SLAB, TO REMAIN
- NEW SLAB

SK#19
One page
One Query
Date: 06-27-2025

DOB STAMP

1250 Maryland Avenue
1250 MARYLAND AVENUE SW
WASHINGTON, DC 20024

BEYER BLINDER BELLE
3307 M Street Northwest, Suite 301
Washington, DC, 20007
202 333 8000

MECHANICAL & PLUMBING
HURST ENGINEERS
703-534-7872

ELECTRICAL
POWER DESIGN INC.
727-497-9811

STRUCTURAL
RATHGEBER GOSS ASSOCIATES
301-590-0071

CIVIL
GORDON DC
202-869-1600

LANDSCAPE
OVS
202-546-7575

INTERIORS
KTGY SDDG
312-274-0707

LIGHTING
CM KLING + ASSOCIATES
703-684-6270

KEY PLAN

STAMP

NO	DATE	DESCRIPTION
4	6/6/25	ISSUED FOR CONSTRUCTION
2	Date5	ADDENDUM 02

REVISIONS

SUBMITTAL

ISSUED FOR CONSTRUCTION

DRAWING TITLE

SLAB EDGE - LEVEL 09 TO 10

SCALE	As indicated
DATE	05/16/25
PROJECT NUMBER	6415.00
DRAWING NUMBER	A057

of

Autodesk Docs://6415 - 1250 Maryland Avenue/X/6415-1250 Maryland Ave-A24.rvt

6/4/2025 6:16:19 PM