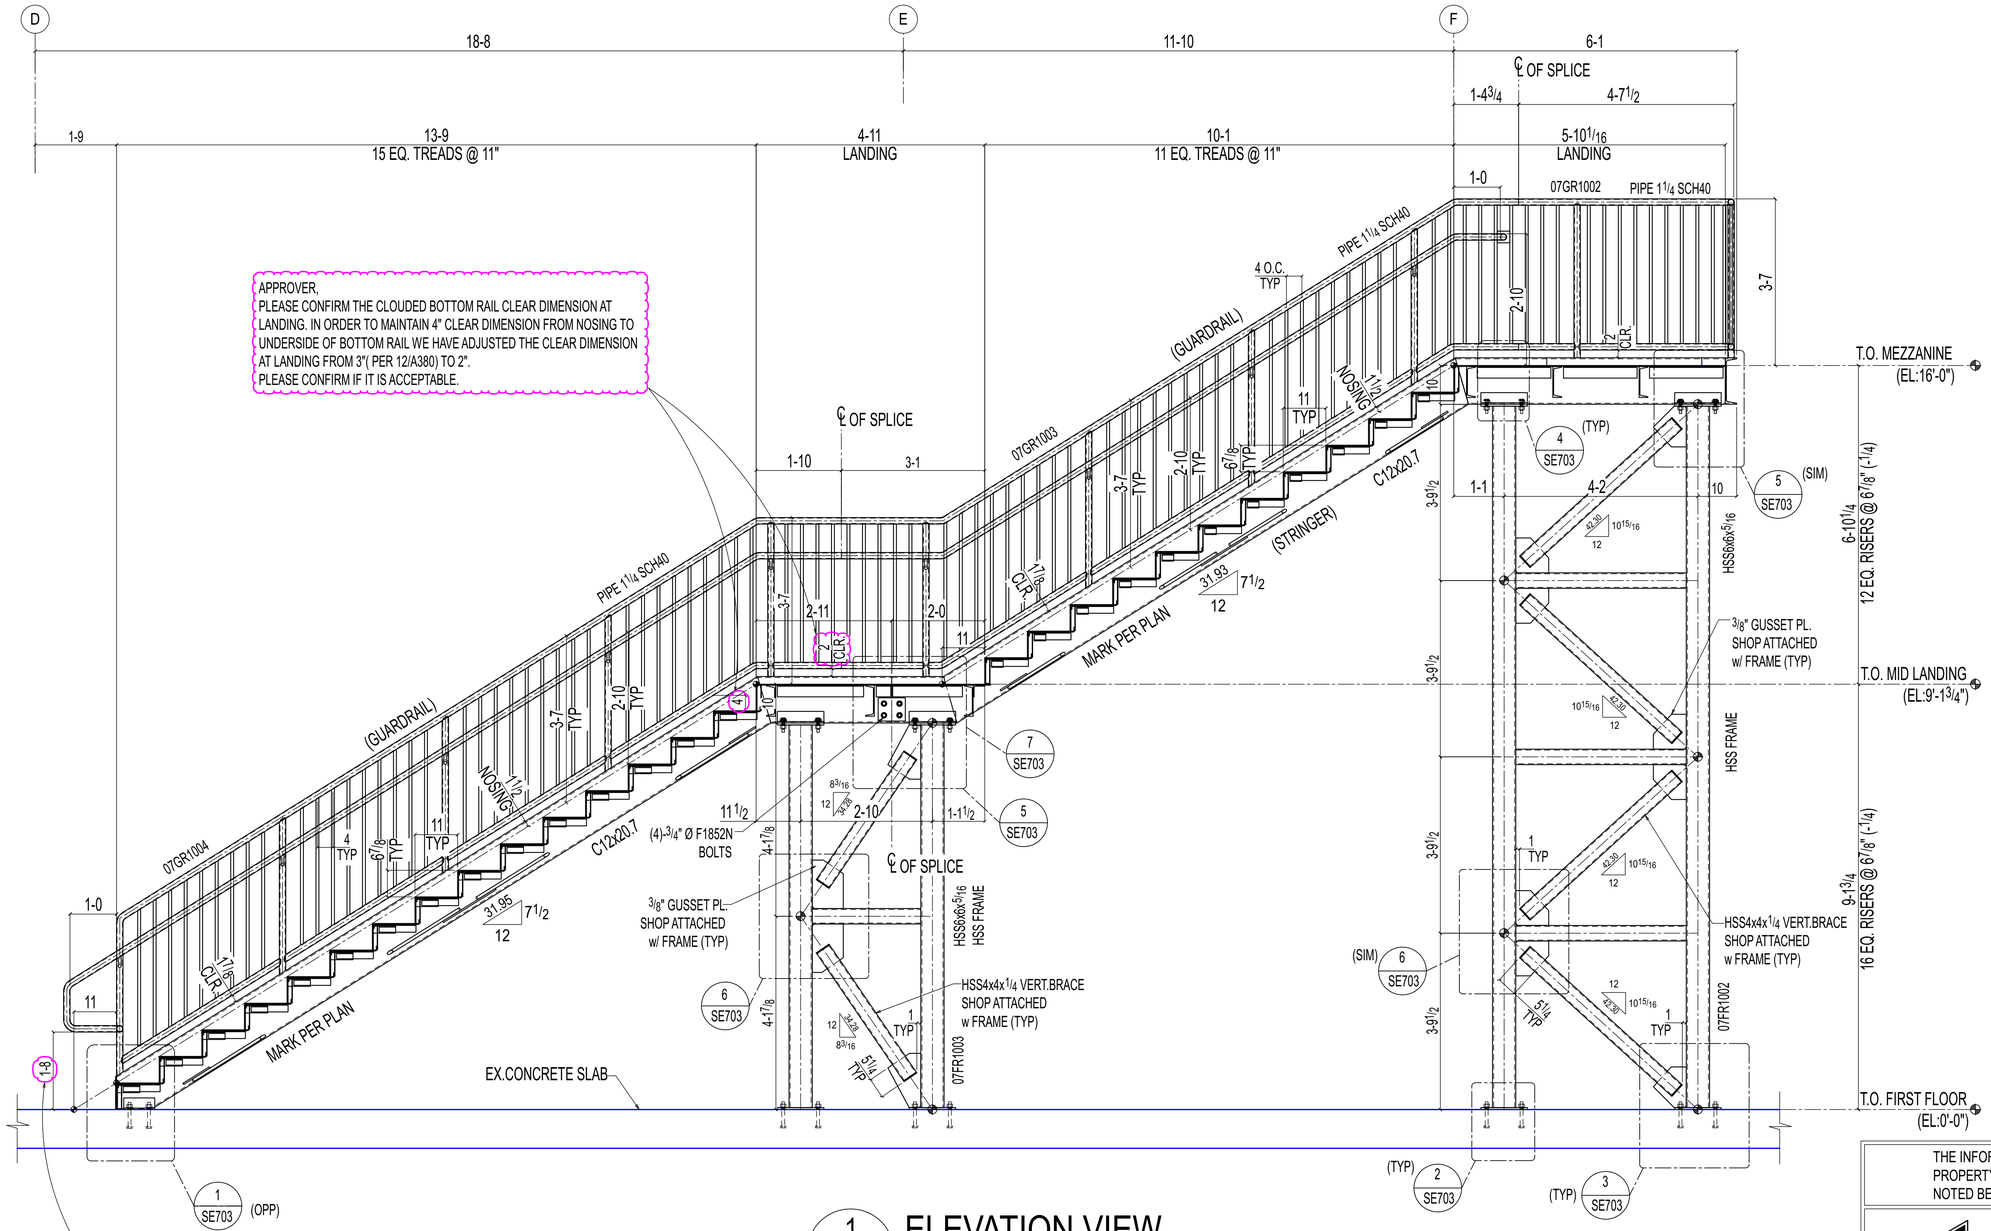

APPROVER,
PLEASE CONFIRM THE CLOUDED BOTTOM RAIL CLEAR DIMENSION AT LANDING. IN ORDER TO MAINTAIN 4" CLEAR DIMENSION FROM NOSING TO UNDERSIDE OF BOTTOM RAIL WE HAVE ADJUSTED THE CLEAR DIMENSION AT LANDING FROM 3"(PER 12/A380) TO 2".
PLEASE CONFIRM IF IT IS ACCEPTABLE.

APPROVER,
PLEASE CONFIRM THE CLOUDED HANDRAIL CLEAR DIMENSION FROM FINISH FLOOR.

1 / SE702 **ELEVATION VIEW**

(REF: 3/A380)

OTHER NOT SHOWN FOR CLARITY

REVISIONS

REV#	DWN BY	DESCRIPTION	DATE
A	SRP	ISSUED FOR APPROVAL	Jun 16 2025

THE INFORMATION NOTED HEREON THIS DRAWING IS THE PROPERTY OF STEEL FAB ENTERPRISES, INC. AND SHALL NOTED BE USED WITHOUT WRITTEN CONSENT.

STEEL FAB
ENTERPRISES, LLC
AISC CERTIFIED FABRICATOR AND ERECTOR
MISCELLANEOUS METALS FABRICATOR AND ERECTORS
623 BAUMGARDNER ROAD, LANCASTER, PA 17603
TEL. (717)464-0330 FAX (717)464-9464
WWW.STEELFABENTERPRISES.COM

PROJECT OWNER : CK CAPITAL, LLC
PROJECT DESCRIPTION : CLEVELAND BROTHERS-MILESBURG
PROJECT ADDRESS : 1025N. EAGLE VALLEY ROAD, HOWARD, PA 16841
CONTRACTOR : KINSLEY CONSTRUCTION, INC.

DRAWN BY : BAS	DATE : 5-20-25	PROJ. NO. : 25012	REV # A
CHECKED BY : SRP	DATE : 5-20-25	DWG NO. : SE702	

DWG DESCRIPTION : ELEVATION VIEW