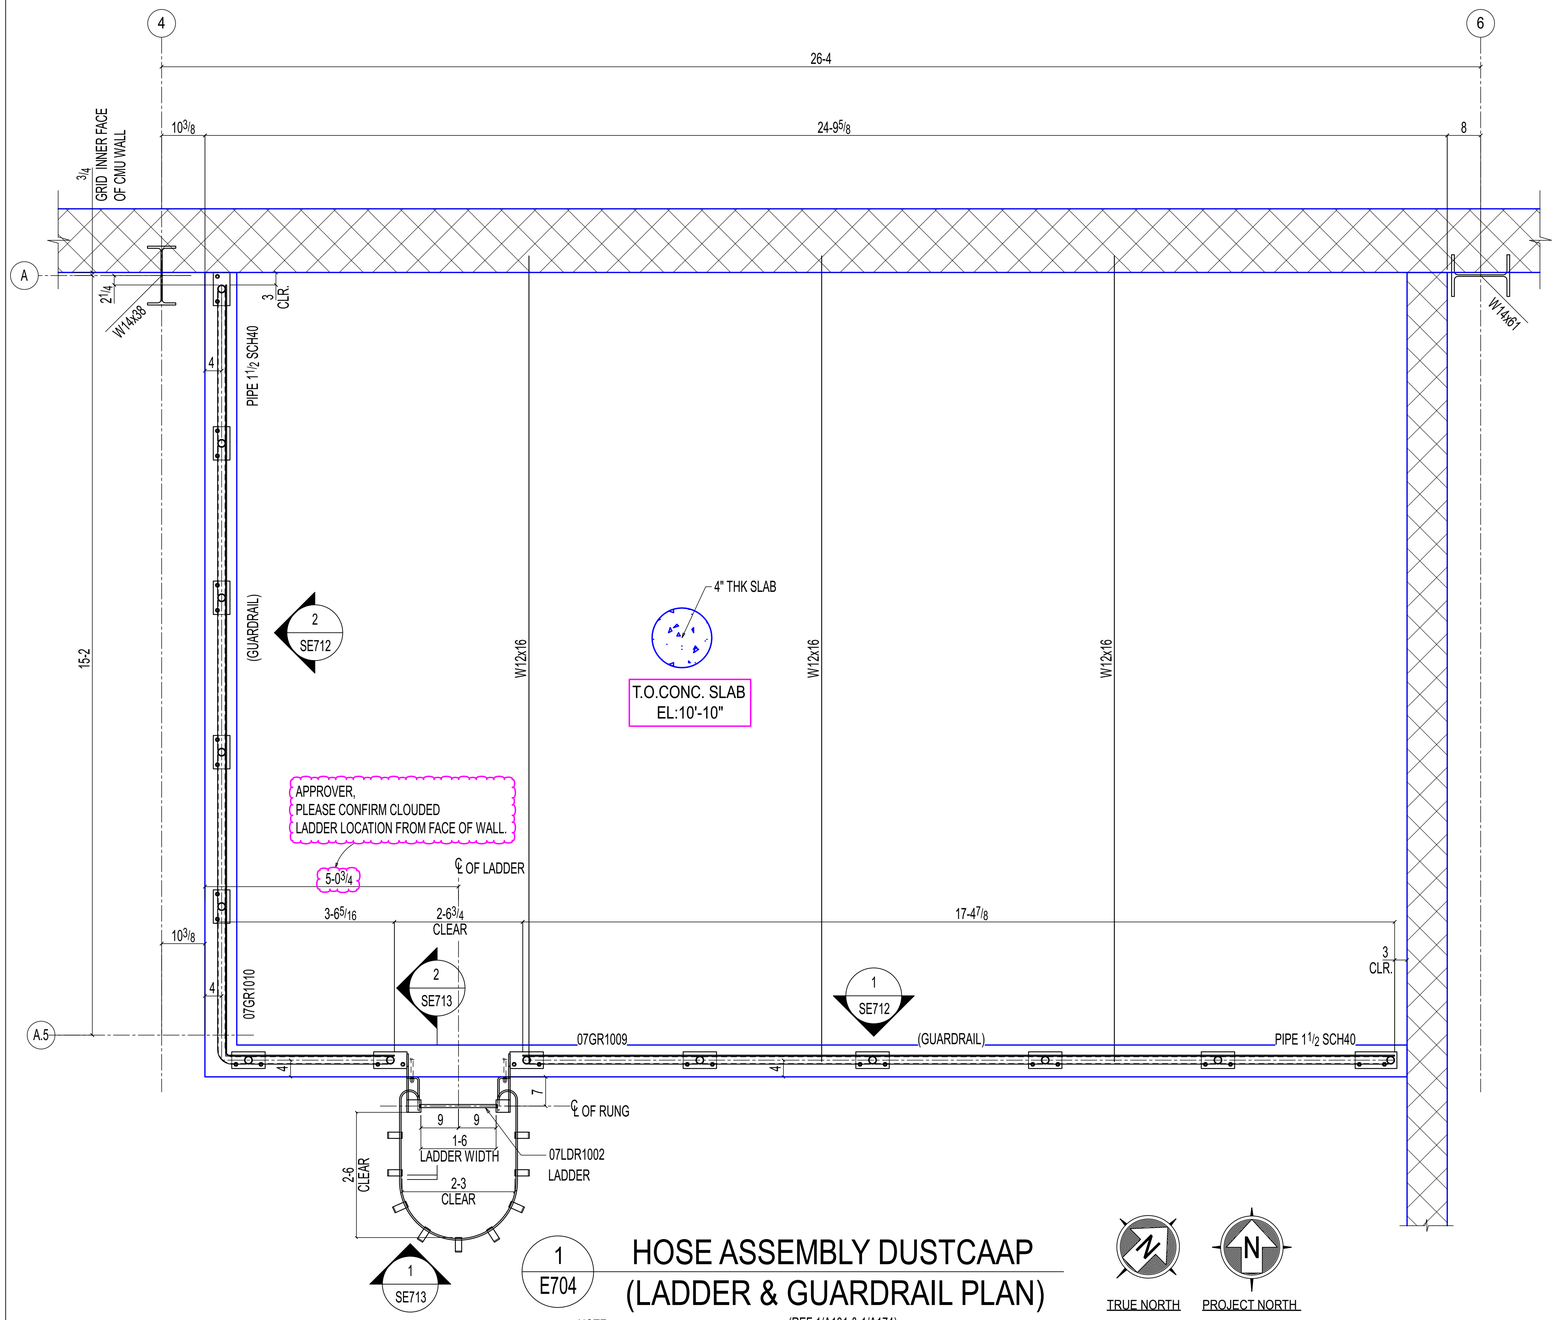

HOSE ASSEMBLY DUSTCAAP (LADDER & GUARDRAIL PLAN)

(REF:1/A101 & 1/A174)

TRUE NORTH PROJECT NORTH

NOTE:
1. ALL ELEVATION ARE REFERENCED FROM THE FINISHED FLOOR EL: [0'-0"] = DATUM EL:100'-0" (U.N.O).
2. ALL GUARDRAILS ARE PIPE 1 1/2 SCH40 (U.N.O).

APPROVER,
WE HAVE FOLLOWED 1 1/2" SCH 40 PIPE FOR
THE FLOOR GUARDRAILS.PLEASE CONFIRM IF IT IS IT OK TO PROCEED?

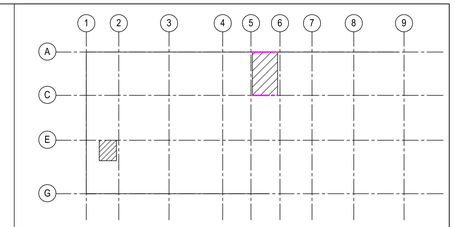

KEY PLAN

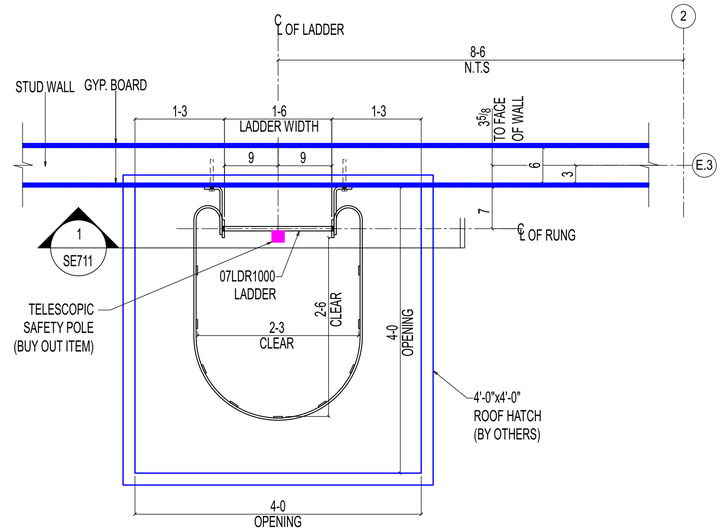

MEZZANINE ROOF ACCESS LADDER

2 / E704

(REF:1/A102 & 3/S411)

TRUE NORTH PROJECT NORTH

REVISIONS

REV#	DWN BY	DESCRIPTION	DATE
A	SRP	ISSUED FOR APPROVAL	Jun 16 2025

THE INFORMATION NOTED HEREON THIS DRAWING IS THE PROPERTY OF STEEL FAB ENTERPRISES, INC. AND SHALL NOTED BE USED WITHOUT WRITTEN CONSENT.

STEEL FAB ENTERPRISES, LLC
AISC CERTIFIED FABRICATOR AND ERECTOR
MISCELLANEOUS METALS FABRICATOR AND ERECTORS
623 BAUMGARDNER ROAD, LANCASTER, PA 17603
TEL. (717)464-0330 FAX (717)464-9464
WWW.STEELFABENTERPRISES.COM

PROJECT OWNER : CK CAPITAL, LLC

PROJECT DESCRIPTION : CLEVELAND BROTHERS-MILESBURG

PROJECT ADDRESS : 4025N. EAGLE VALLEY ROAD, HOWARD, PA 16841

CONTRACTOR : KINSLEY CONSTRUCTION, INC.

DRAWN BY : BAS	DATE : 5-20-25	PROJ. NO. : 25012	REV # A
CHECKED BY : SRP	DATE : 5-20-25	DWG NO. : E704	

DWG DESCRIPTION : HOSE ASSEMBLY DUSTCAAP (LADDER & HUARDRAIL PLAN)