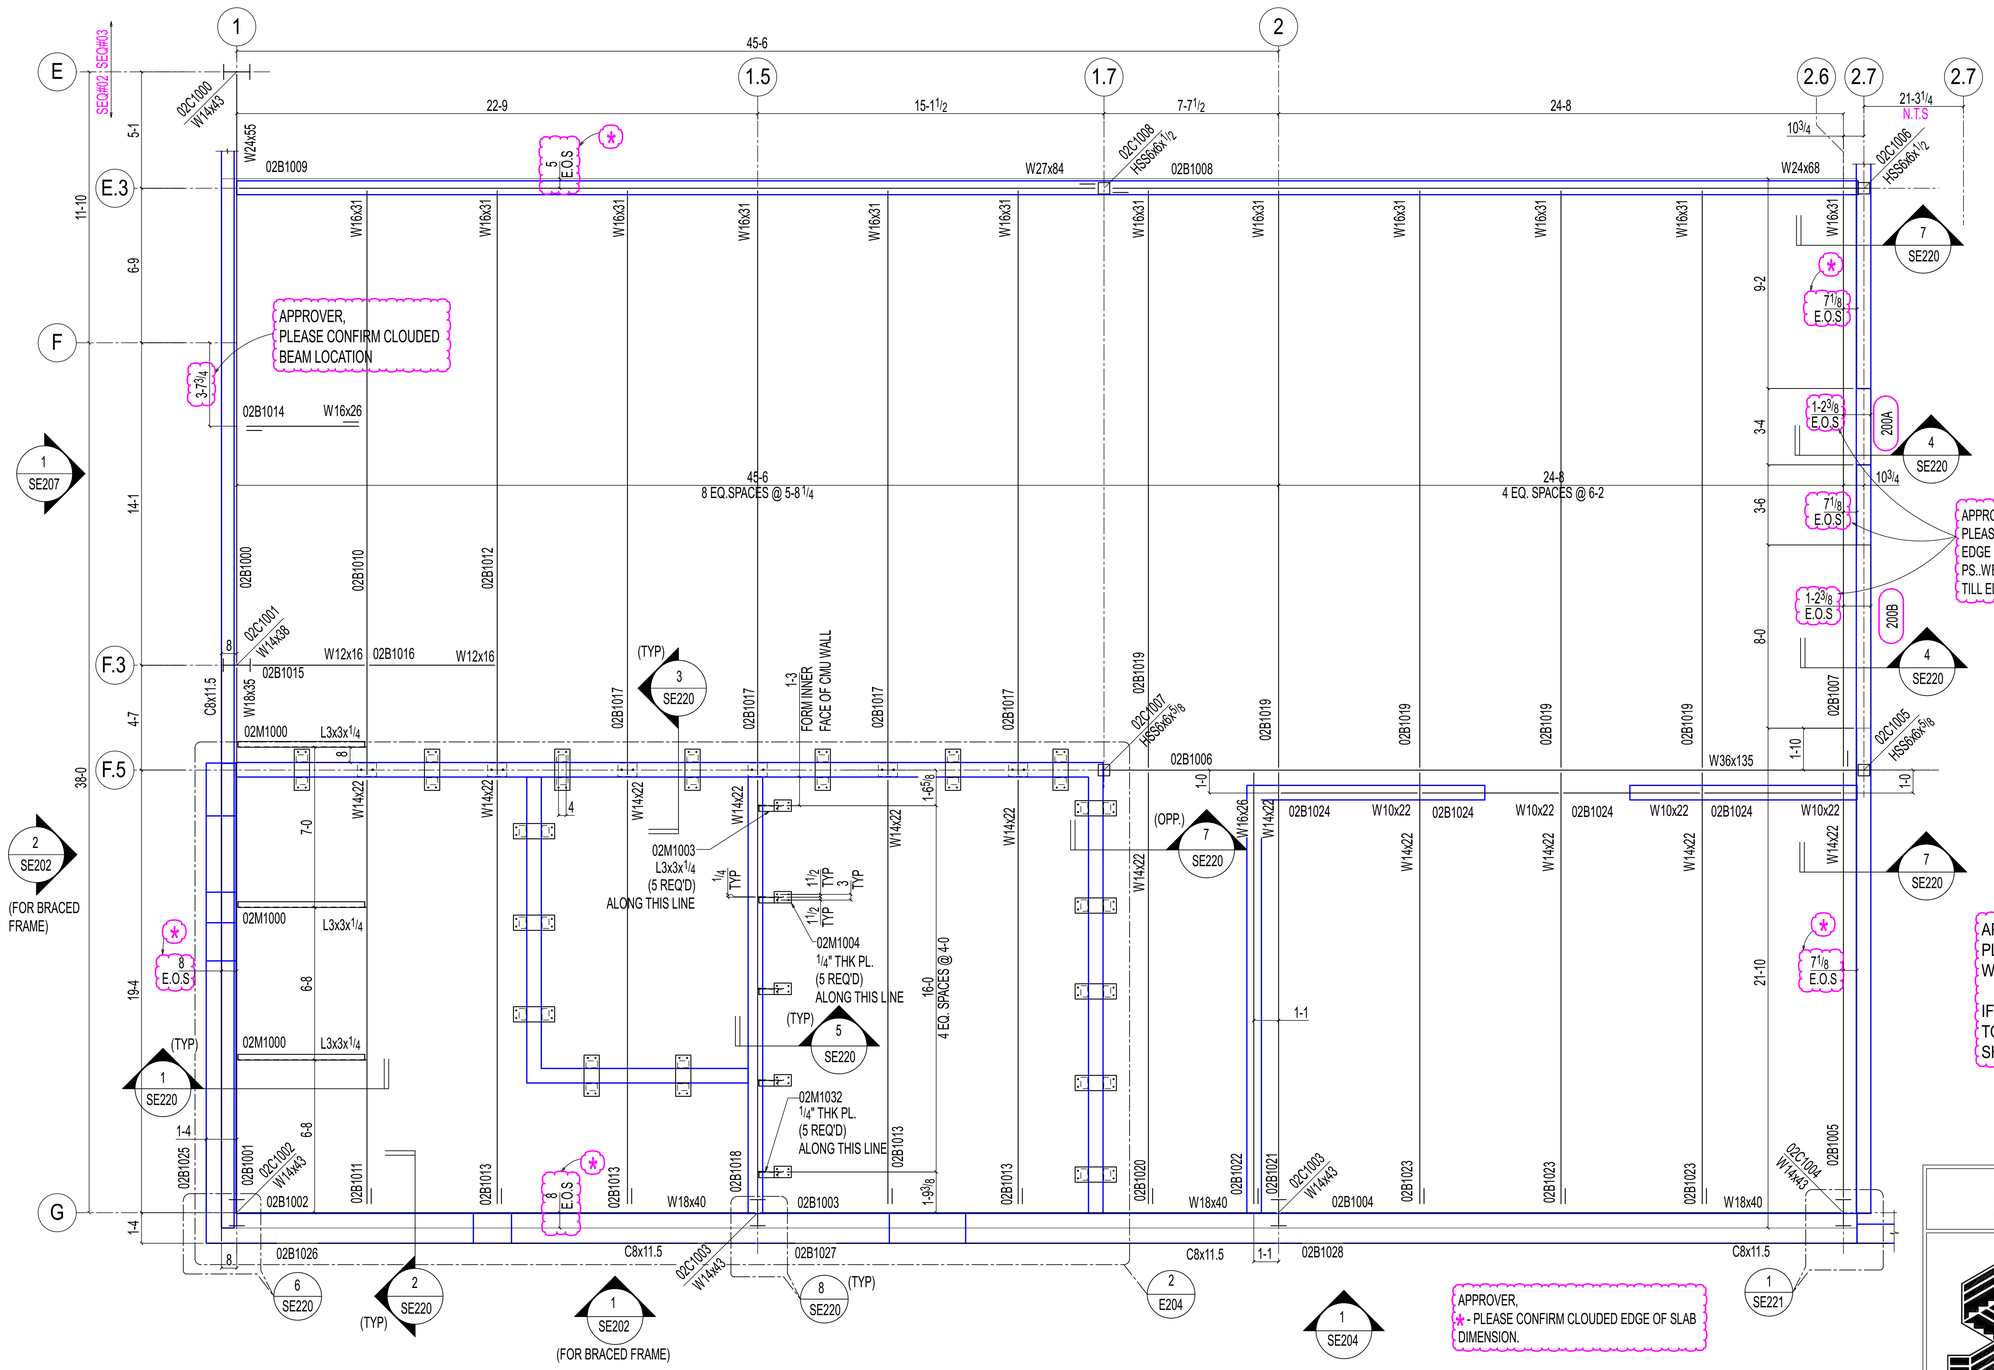

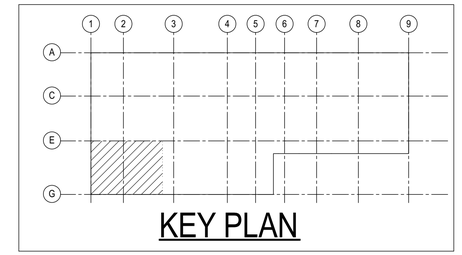

APPROVER
PLEASE CONFIRM ALL STEEL IN THIS MEZZANINE AREA
WILL RECIEVE FIREPROOFING AND WILL BE NO PAINTED.

IF FIREPROOFED COLUMNS RUNS THROUGH MEZZANINE LEVEL
TO ROOF WILL BE FIREPROOFED TILL MEZZANINE LEVEL AND
SHOP PRIMED ABOVE MEZZANINE LEVEL. PLEASE CONFIRM.

1 / E202 MEZZANINE FRAMING PLAN (SEQ#02)

(REF: 1/S102,1/A102)

1. TOP OF MEZZANINE FLOOR SLAB ELEVATION = 16'-0" (U.N.O).
2. TOP OF MEZZANINE STEEL ELEVATION =15'-8" (U.N.O) ALL ELEVATION
   REFFERED FROM FINISHED FLOOR ELEVATION [0'-0"] = DATUM ELEVATION 100'-0" (U.N.O)
3. ALL FIELD BOLTS SHALL BE 3/4" Ø F1852N TC BOLTS.(U.N.O).
4. (1)-DENOTES 1"Ø F2280N TC BOLTS.
5. SEE SHEET SE228 FOR TYPICAL CMU WALL BRACING DETAIL.

TRUE NORTH PROJECT NORTH

REVISIONS

REV#	DWN BY	DESCRIPTION	DATE
A	SRP	ISSUED FOR APPROVAL	Jun 11 2025

THE INFORMATION NOTED HEREON THIS DRAWING IS THE PROPERTY OF STEEL FAB ENTERPRISES, INC. AND SHALL NOTED BE USED WITHOUT WRITTEN CONSENT.

STEEL FAB
ENTERPRISES, LLC
AISC CERTIFIED FABRICATOR AND ERECTOR
MISCELLANEOUS METALS FABRICATOR AND ERECTORS
623 BAUMGARDNER ROAD, LANCASTER, PA 17603
TEL. (717)464-0330 FAX (717)464-9464
WWW.STEELFABENTERPRISES.COM

PROJECT OWNER : CK CAPITAL, LLC
PROJECT DESCRIPTION : CLEVELAND BROTHERS-MILESBURG
PROJECT ADDRESS : 1025N. EAGLE VALLEY ROAD, HOWARD, PA 16841
CONTRACTOR : KINSLEY CONSTRUCTION, INC.

DRAWN BY : BAS	DATE : 5-20-25	PROJ. NO. :	25912	REV # A
CHECKED BY : SRP	DATE : 5-20-25	DWG NO. :	E202	

DWG DESCRIPTION : MEZZANINE FRAMING PLAN