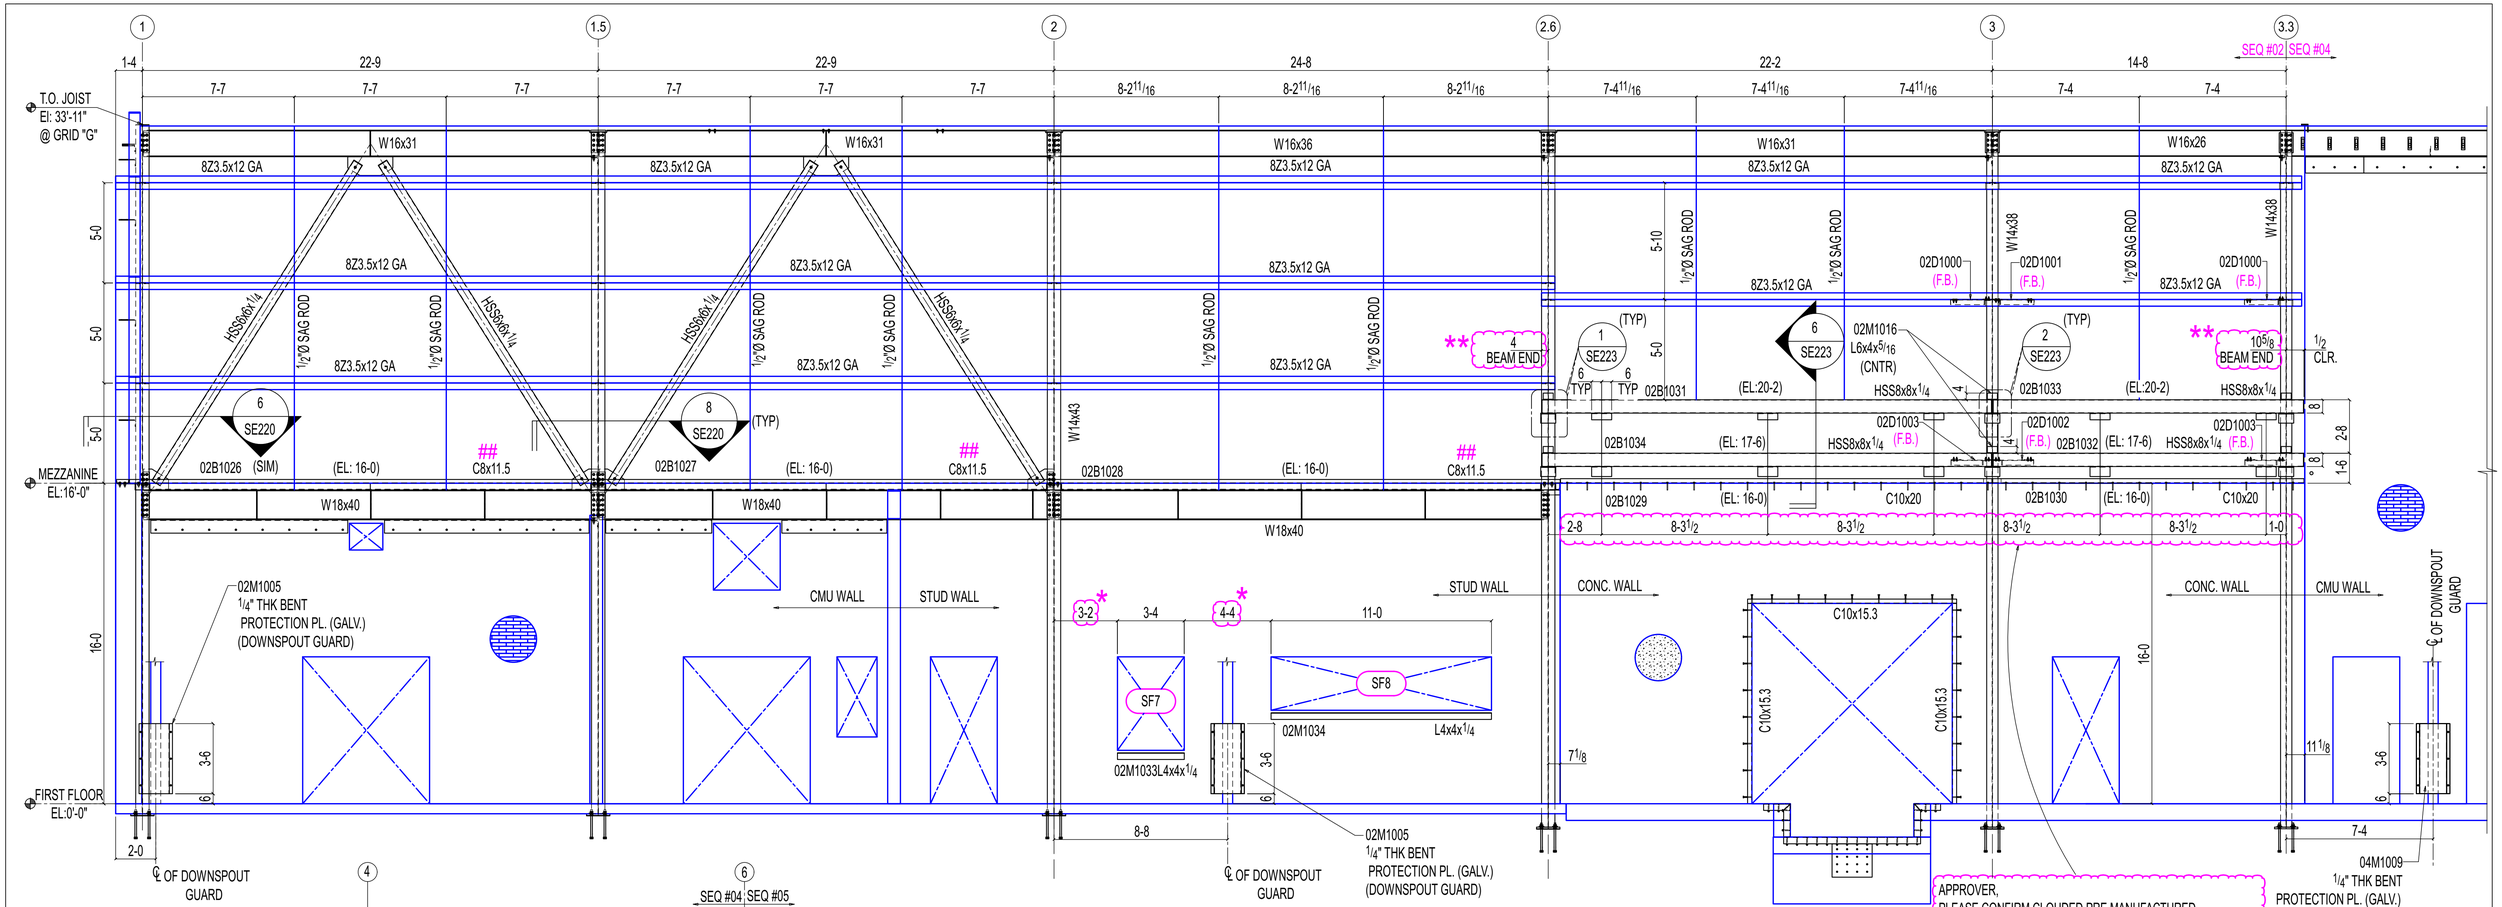

1 SE204 ELEVATION VIEW- SOUTH

(REF: 1/S102,2/S200)

OTHER NOT SHOWN FOR CLARITY

NOTES:
1.ALL SHOWN ELEVATIONS ARE REFERENCED FROM FINISHED FLOOR ELEVATION (EL:0'-0") = DATUM EL:100'-0" (U.N.O).
2. (F.B.) -DENOTES FLANGE BRACE AT COLUMN. SEE SHEET SE228 FOR TYPICAL SECTION.
3.REFER SHEET SE226 FOR TYPICAL SECTIONS.

APPROVER,
PLEASE CONFIRM IF ANY ADDITIONAL FLANGE BRACE NEEDED OTHER THAN SHOWN ON THIS PLAN INDICATED F.B

##- ERECTOR NOTE:
ERECT THIS CHANNEL BEFORE CMU WALL CONSTRUCTION.

ERECTOR NOTE:
1.FIELD DRILL HOLES IN CHANNEL AND HSS BEAMS FOR SAG ROD CONNECTION.

APPROVER,
PLEASE CONFIRM CLOUDED PRE MANUFACTURED CANOPY SUPPORT ANGLE LOCATIONS ARE OK TO PROCEED?

** -APPROVER,
PLEASE CONFIRM CLOUDED BEAM EXTEND DIMENSIONS ARE OK TO PROCEED?

* - APPROVER,
PLEASE CONFIRM CLOUDED STOREFRONT SUPPORT ANGLE LOCATIONS ARE OK TO PROCEED?

LEGEND
---CMU WALL
---CONCRETE WALL

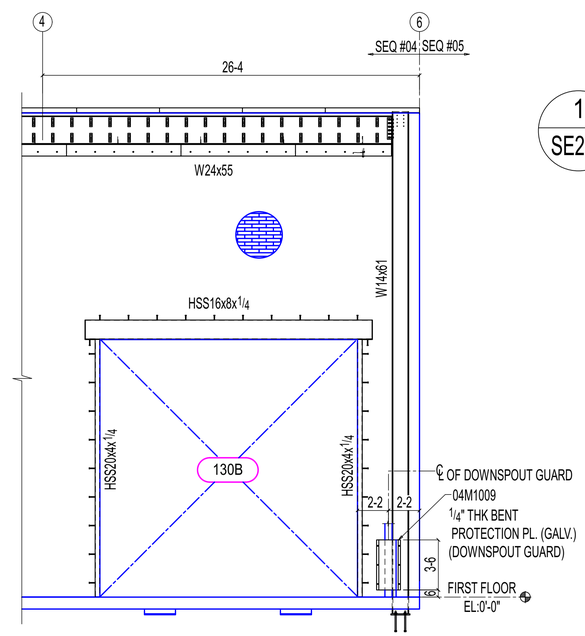

2 SE204 ELEVATION VIEW- SOUTH

(REF: 1/S102,2/S200)

OTHER NOT SHOWN FOR CLARITY

NOTES:
1.ALL SHOWN ELEVATIONS ARE REFERENCED FROM FINISHED FLOOR ELEVATION (EL:0'-0") = DATUM EL:100'-0" (U.N.O).

REVISIONS

REV#	DWN BY	DESCRIPTION	DATE
A	SRP	ISSUED FOR APPROVAL	Jun 11 2025

THE INFORMATION NOTED HEREON THIS DRAWING IS THE PROPERTY OF STEEL FAB ENTERPRISES, INC. AND SHALL NOTED BE USED WITHOUT WRITTEN CONSENT.

STEEL FAB
ENTERPRISES, LLC
MISCELLANEOUS METALS FABRICATOR AND ERECTORS
623 BAUMGARDNER ROAD, LANCASTER, PA 17603
TEL. (717)464-0330 FAX (717)464-9464
WWW.STEELFABENTERPRISES.COM

AISC CERTIFIED FABRICATOR AND ERECTOR

PROJECT OWNER : CK CAPITAL, LLC
PROJECT DESCRIPTION : CLEVELAND BROTHERS-MILESBURG
PROJECT ADDRESS : 1025N. EAGLE VALLEY ROAD, HOWARD, PA 16841
CONTRACTOR : KINSLEY CONSTRUCTION, INC.

DRAWN BY : BAS	DATE : 05-20-25	PROJ. NO. : 25012	REV # A
CHECKED BY : SRP	DATE : 05-20-25	DWG NO. : SE204	

DWG DESCRIPTION : ELEVATION VIEW