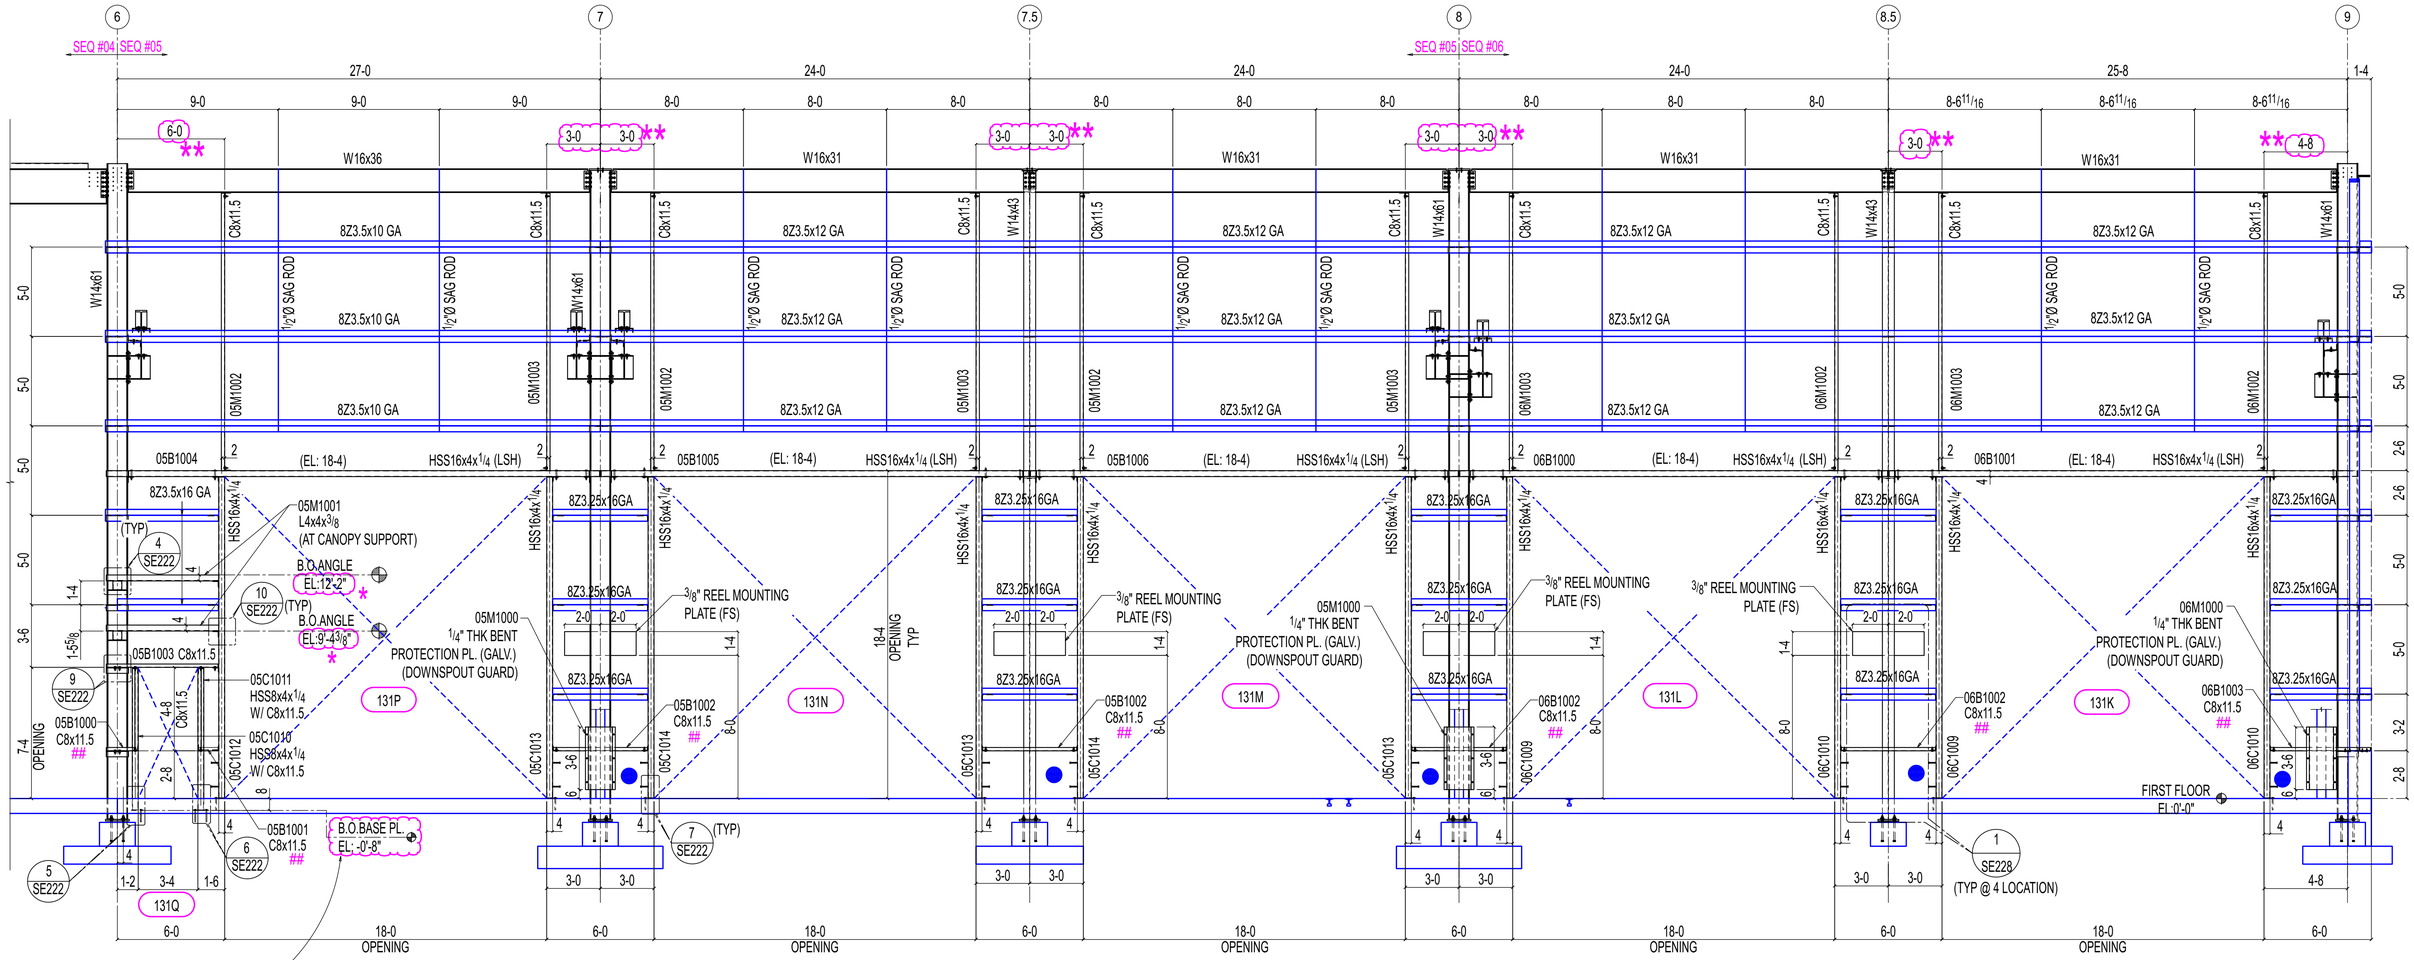

APPROVER,
PLEASE CONFIRM CLOUDED BOTTOM BASE PLATE
ELEVATION FOR THE HSS8X4 POST IS OKAY TO PROCEED.

* -APPROVER,
PLEASE CONFIRM CLOUDED PRE MANUFACTURED
CANOPY SUPPORT ANGLE ELEVATIONS ARE OK TO PROCEED?

** -APPROVER,
PLEASE CONFIRM ALL CLOUDED CHANNEL
LOCATIONS ARE OK TO PROCEED?

1 / SE205

ELEVATION VIEW- SOUTH

(REF: 1/S102,2/S200)

OTHER NOT SHOWN FOR CLARITY

NOTES:
1. ALL SHOWN ELEVATIONS ARE REFERENCED FROM FINISHED FLOOR ELEVATION (EL:0'-0") = DATUM EL:100'-0" (U.N.O).
2. REFER SHEET SE226 FOR TYPICAL SECTIONS.
3. ALL DOOR FRAME STEELS ARE GALVANIZED (U.N.O)

##- ERECTOR NOTE:
ERECT THIS CHANNEL BEFORE CMU WALL CONSTRUCTION.

ERECTOR NOTE:
1. FIELD DRILL HOLES IN CHANNEL AND HSS BEAMS FOR SAG ROD CONNECTION.

LEGEND

---CMU WALL

REVISIONS

REV#	DWN BY	DESCRIPTION	DATE
A	SRP	ISSUED FOR APPROVAL	Jun 11 2025

THE INFORMATION NOTED HEREON THIS DRAWING IS THE PROPERTY OF STEEL FAB ENTERPRISES, INC. AND SHALL NOTED BE USED WITHOUT WRITTEN CONSENT.

STEEL FAB
ENTERPRISES, LLC
AISC CERTIFIED FABRICATOR AND ERECTOR
MISCELLANEOUS METALS FABRICATOR AND ERECTORS
623 BAUMGARDNER ROAD, LANCASTER, PA 17603
TEL. (717)464-0330 FAX (717)464-9464
WWW.STEELFABENTERPRISES.COM

PROJECT OWNER : CK CAPITAL, LLC
PROJECT DESCRIPTION : CLEVELAND BROTHERS-MILESBURG
PROJECT ADDRESS : 1025N. EAGLE VALLEY ROAD, HOWARD, PA 16841
CONTRACTOR : KINSLEY CONSTRUCTION, INC.

DRAWN BY : BAS	DATE : 05-20-25	PROJ. NO. : 25012	REV # A
CHECKED BY : SRP	DATE : 05-20-25	DWG NO. : SE205	
DWG DESCRIPTION : ELEVATION VIEW			