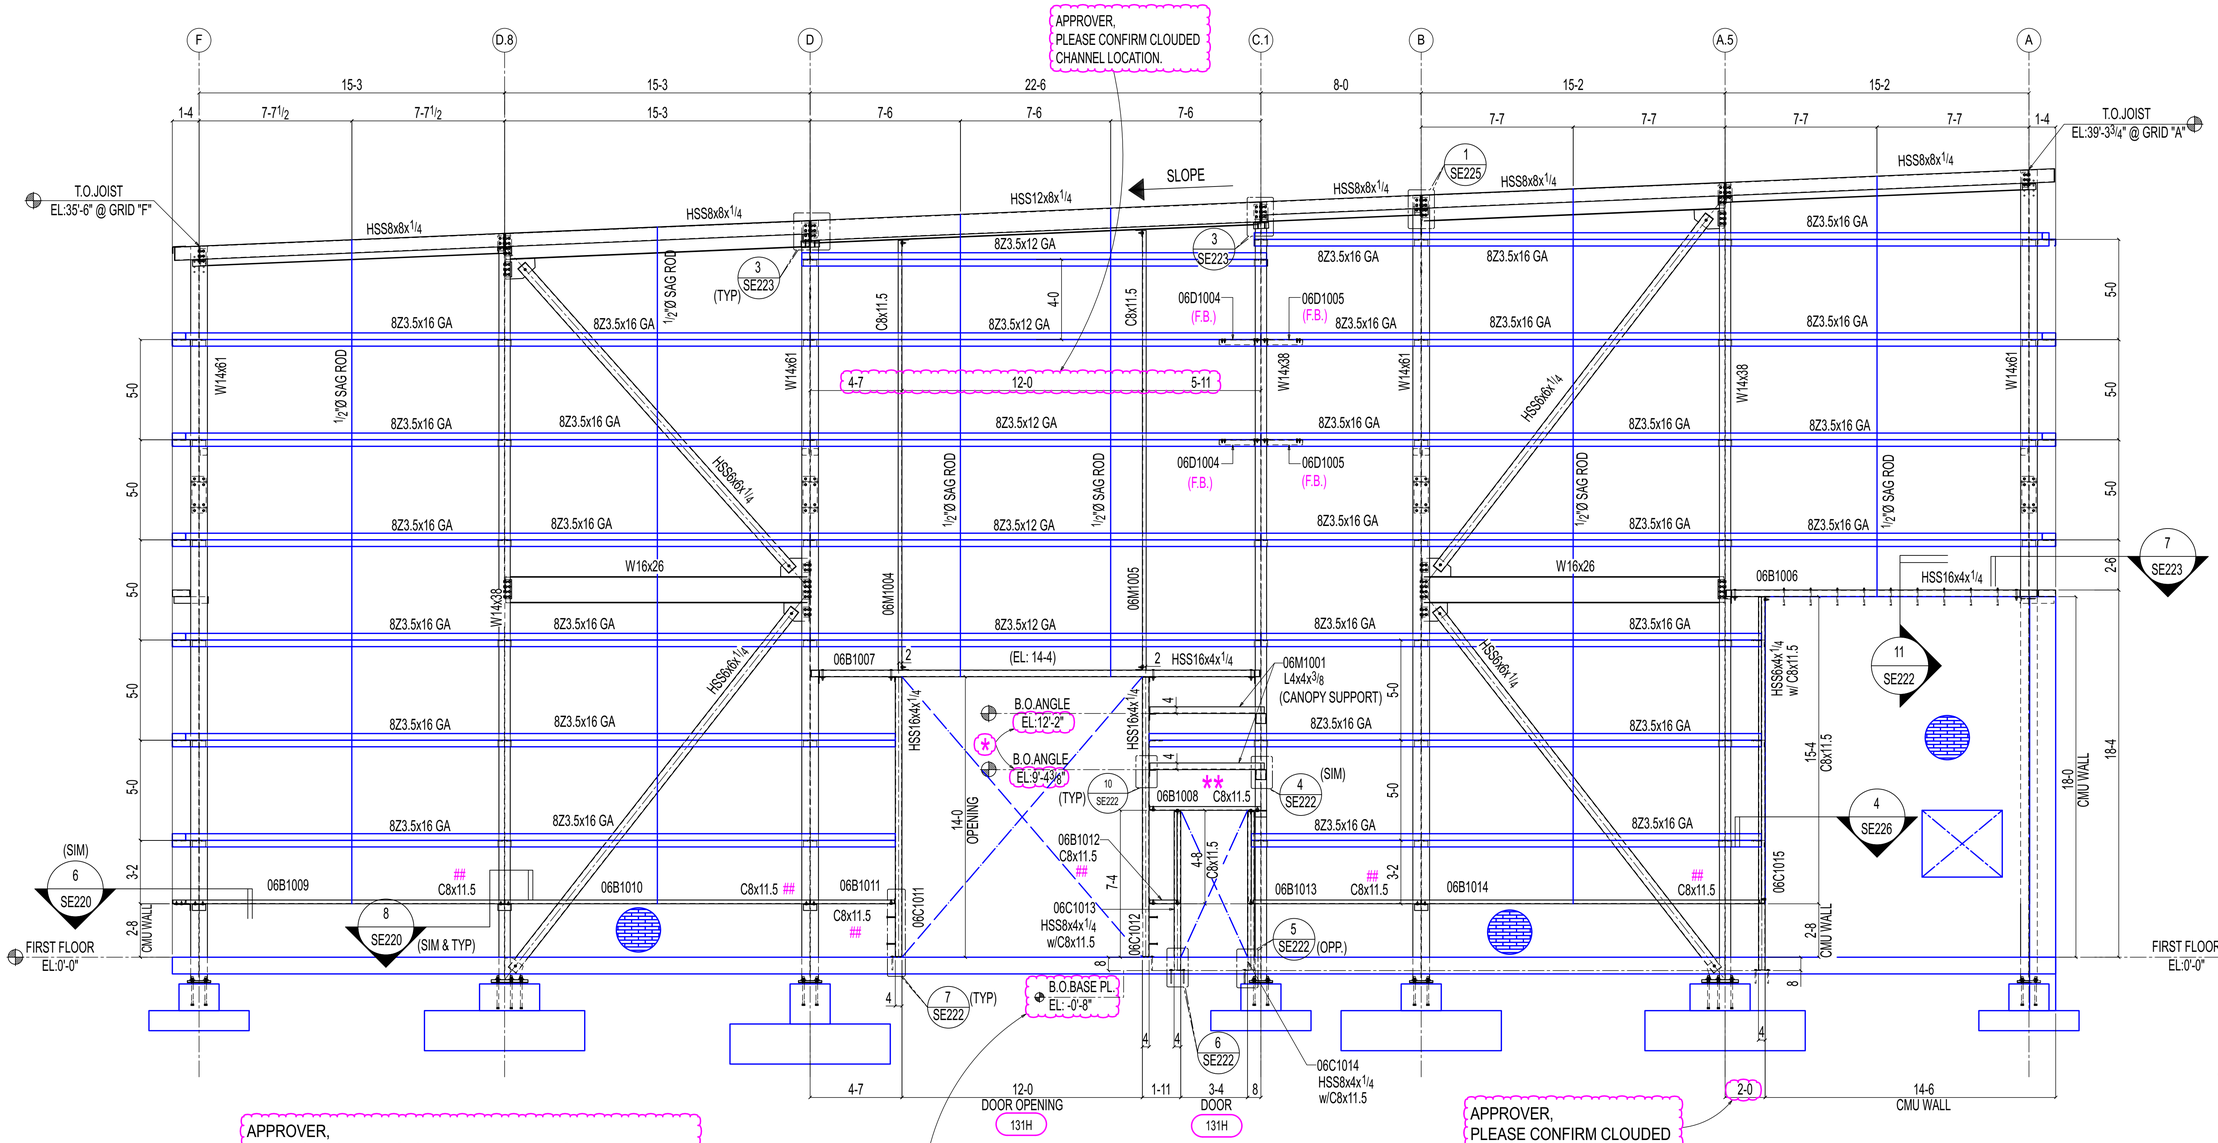

APPROVER,
* -PLEASE CONFIRM CLOUDED PRE MANUFACTURED CANOPY SUPPORT ANGLE ELEVATIONS ARE OK TO PROCEED?

** -APPROVER,
PLEASE ADVISE WHEATHER WE NEED TO PROVIDE HSS TUBE PER ARCH DRAWING A515(H-10 HEAD) SINCE STRUCTURAL DRAWING ONLY SHOWS CHANNEL AT THIS LOCATION.

APPROVER,
PLEASE CONFIRM CLOUDED BOTTOM BASE PLATE ELEVATION FOR THE HSS8X4 AND HSS6x4 POST ARE OKAY TO PROCEED.

APPROVER,
PLEASE CONFIRM CLOUDED HSS POST LOCATION.

1 / SE206 ELEVATION VIEW-EAST

(REF: 1/S102,3/S200)

OTHER NOT SHOWN FOR CLARITY

##- ERECTOR NOTE:
ERECT THIS CHANNEL BEFORE CMU WALL CONSTRUCTION.

LEGEND

---CMU WALL

NOTES:
1.ALL SHOWN ELEVATIONS ARE REFERENCED FROM FINISHED FLOOR ELEVATION (EL:0'-0") = DATUM EL:100'-0" (U.N.O).
2. (F.B.) -DENOTES FLANGE BRACE AT COLUMN. SEE SHEET SE228 FOR TYPICAL SECTION.
3.REFER SHEET SE226 FOR TYPICAL SECTIONS.

APPROVER,
PLEASE CONFIRM IF ANY ADDITIONAL FLANGE BRACE NEEDED OTHER THAN SHOWN ON THIS PLAN INDICATED F.B.

REVISIONS

REV#	DWN BY	DESCRIPTION	DATE
A	SRP	ISSUED FOR APPROVAL	Jun 11 2025

THE INFORMATION NOTED HEREON THIS DRAWING IS THE PROPERTY OF STEEL FAB ENTERPRISES, INC. AND SHALL NOT BE USED WITHOUT WRITTEN CONSENT.

STEEL FAB
ENTERPRISES, LLC
AISC CERTIFIED FABRICATOR AND ERECTOR
MISCELLANEOUS METALS FABRICATOR AND ERECTORS
623 BAUMGARDNER ROAD, LANCASTER, PA 17603
TEL. (717)464-0330 FAX (717)464-9464
WWW.STEELFABENTERPRISES.COM

PROJECT OWNER : CK CAPITAL, LLC
PROJECT DESCRIPTION : CLEVELAND BROTHERS-MILESBURG
PROJECT ADDRESS : 1025N. EAGLE VALLEY ROAD, HOWARD, PA 16841
CONTRACTOR : KINSLEY CONSTRUCTION, INC.

DRAWN BY : BAS	DATE : 05-20-25	PROJ. NO. : 25012	REV # A
CHECKED BY : SRP	DATE : 05-20-25	DWG NO. : SE206	

DWG DESCRIPTION : ELEVATION VIEW