NOTE IF THIS SHEET IS NOT 36"W x 48"D THEN IT IS NOT THE INTENDED SIZE. IN ALL CASES, WORK TO FIGURED DIMENSIONS.

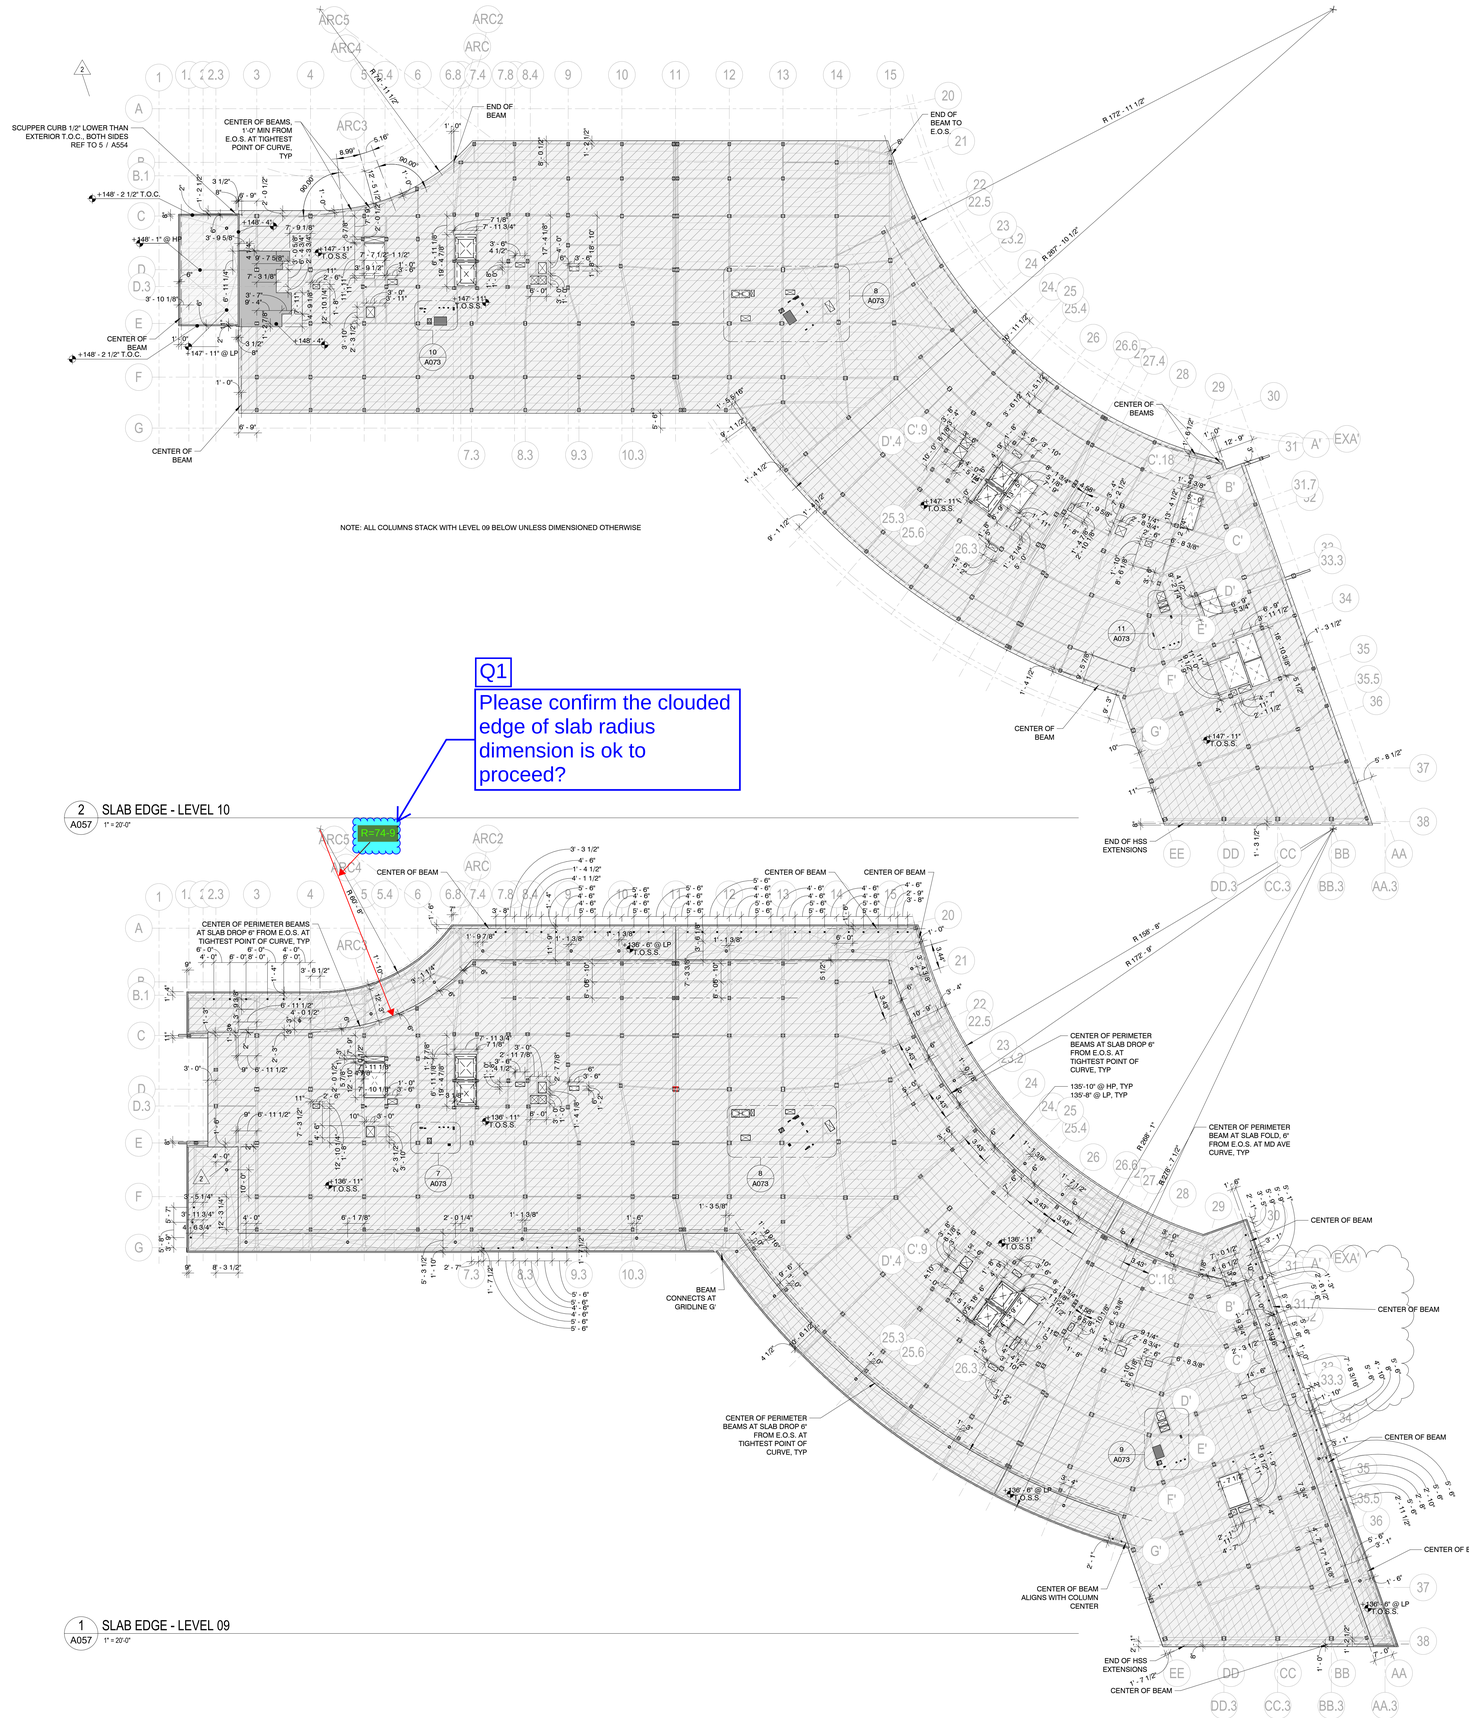

Q1

Please confirm the clouded edge of slab radius dimension is ok to proceed?

2 A057 SLAB EDGE - LEVEL 10
1" = 20'-0"

1 A057 SLAB EDGE - LEVEL 09
1" = 20'-0"

NEW FLOOR STEEL STRUCTURE NOTES:

1. SEE STRUCTURAL DRAWINGS FOR STEEL SIZING & LOCATIONS
2. NEW STEEL COLUMNS ALIGNED W/ EXISTING CONCRETE COLUMNS BELOW UNLESS NOTED OTHERWISE. DIMENSIONS PROVIDED FOR COLUMNS NOT ALIGNED W/ BELOW.
3. SEE STRUCTURAL DRAWINGS FOR STEEL COLUMN SIZING & SHAPE. RECTANGULAR GRAPHIC SHOWN IN ARCHITECTURAL PLANS ALSO REPRESENTS GYPSUM FURRING NEEDED FOR RATING.

LEGEND

- NEW STEEL COLUMN, ALIGNED WITH COLUMN BELOW
- NEW STEEL COLUMN SUPPORTED BY BEAM BELOW, SEE DIMENSIONS

SLAB EDGE DRAWING NOTES:

1. SLAB DRAWINGS ARE BASED ON ORIGINAL EXISTING DRAWINGS. ALL LOCATIONS & DIMENSIONS TO BE VERIFIED IN FIELD. CONTRACTOR TO NOTIFY ARCHITECT OF ANY OPE DRA INF
2. SE NE DE ARE
3. SE DE ELE
4. NE EXT AD. NO
5. SE PER PERIMETER OMMITED FROM THIS

LEGEND

- EXISTING SLAB, TO REMAIN
- NEW SLAB,

SK#13
2 pages
2 **Queries**
Date: 06-27-2025

DOB STAMP

1250 Maryland Avenue
1250 MARYLAND AVENUE SW
WASHINGTON, DC 20024

BEYER BLINDER BELLE
3307 M Street Northwest, Suite 301
Washington, DC, 20007
202 333 8000

MECHANICAL & PLUMBING
HURST ENGINEERS
703-534-7872

ELECTRICAL
POWER DESIGN INC.
727-497-9811

STRUCTURAL
RATHGEBBER GOSS ASSOCIATES
301-590-0071

CIVIL
GORDON DC
202-869-1600

LANDSCAPE
OVS
202-546-7575

INTERIORS
KTGY SDDG
312-274-0707

LIGHTING
CM KLING + ASSOCIATES
703-684-6270

KEY PLAN

STAMP

NO	DATE	DESCRIPTION
4	6/6/25	ISSUED FOR CONSTRUCTION
2	Date6	ADDENDUM 02

REVISIONS

SUBMITTAL

ISSUED FOR CONSTRUCTION

DRAWING TITLE

SLAB EDGE - LEVEL 09 TO 10

SCALE	As indicated
DATE	05/16/25
PROJECT NUMBER	6415.00
DRAWING NUMBER	A057

of

Autodesk Docs://6415 - 1250 Maryland Avenue SW/6415-1250 Maryland Ave-KS4.rvt

6/4/2025 6:16:16 PM

NOTE IF THIS SHEET IS NOT 36"W X 48"D
THEN IT IS NOT THE INTENDED SIZE. IN ALL
CASES, WORK TO FIGURED DIMENSIONS.

0 0.5' 1' 2'

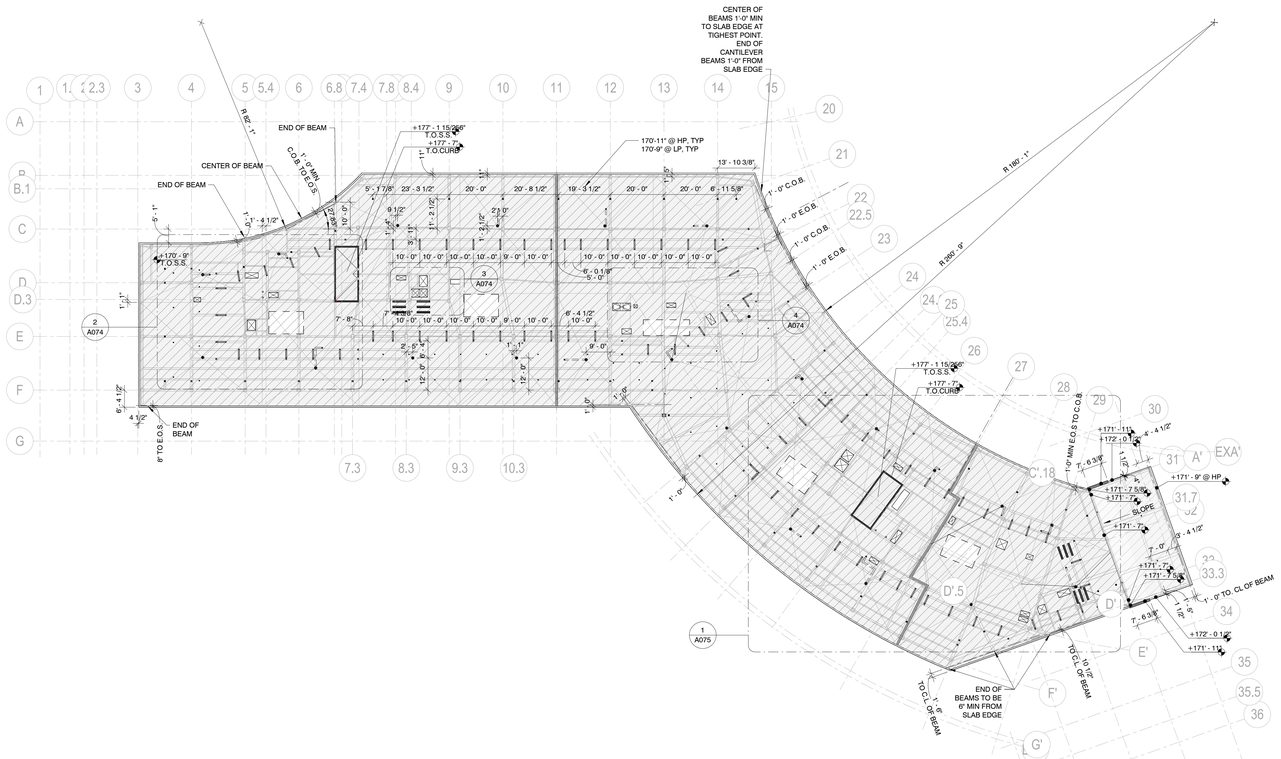

2 A058 SLAB EDGE - ROOF
1" = 20'-0"

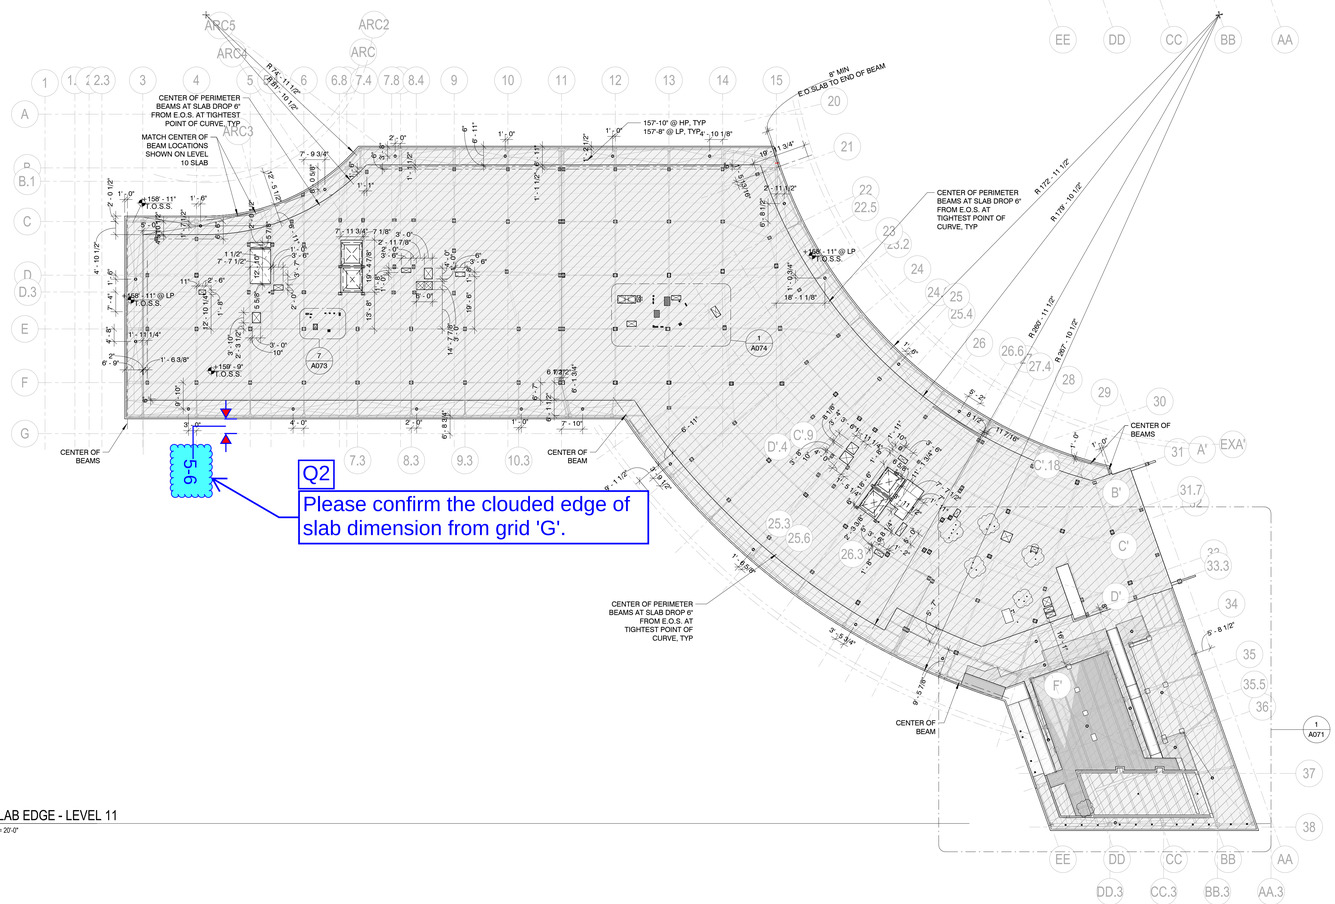

1 A058 SLAB EDGE - LEVEL 11
1" = 20'-0"

NEW FLOOR STEEL STRUCTURE NOTES:

1. SEE STRUCTURAL DRAWINGS FOR STEEL SIZING & LOCATIONS
2. NEW STEEL COLUMNS ALIGNED W/ EXISTING CONCRETE COLUMNS BELOW UNLESS NOTED OTHERWISE. DIMENSIONS PROVIDED FOR COLUMNS NOT ALIGNED W/ BELOW.
3. SEE STRUCTURAL DRAWINGS FOR STEEL COLUMN SIZING & SHAPE. RECTANGULAR GRAPHIC SHOWN IN ARCHITECTURAL PLANS ALSO REPRESENTS GYPSUM FURRING NEEDED FOR RATING.

LEGEND

- NEW STEEL COLUMN, ALIGNED WITH COLUMN BELOW
- NEW STEEL COLUMN SUPPORTED BY BEAM BELOW, SEE DIMENSIONS

SLAB EDGE DRAWING NOTES:

1. SLAB DRAWINGS ARE BASED ON ORIGINAL EXISTING DRAWINGS. ALL LOCATIONS & DIMENSIONS TO BE VERIFIED IN FIELD. CONTRACTOR TO NOTIFY ARCHITECT OF ANY OPENINGS NOT SHOWN ON DRAWINGS. OPENINGS MAY REQUIRE INFILL.
2. SEE DEMOLITION DRAWINGS FOR NEW OPENINGS, STRUCTURAL DEMOLITION, & SLAB EDGES THAT ARE TO BE CUT BACK.
3. SEE ADDITIONAL NOTES ON DEMOLITION DRAWINGS FOR ELEVATOR PITS IN PARKING GARAGE.
4. NEW INFILLS AT OPENINGS & SLAB EXTENSIONS ARE TO MATCH ADJACENT SLAB LEVEL UNLESS NOTED OTHERWISE.
5. SEE A06# SERIES FOR ENLARGED PERIMETER PLANS. DIMENSIONS OF PERIMETER OMMITED FROM THIS DRAWING FOR CLARITY.

LEGEND

- EXISTING SLAB, TO REMAIN
- NEW SLAB, INFILL
- NEW SLAB, DOWEL
- NEW SLAB, CONC ON METAL DECK
- NEW CONCRETE TOPPING FILL
- COLUMN DROP OR BEAM BELOW

0 5' 10' 20' 40'

DOB STAMP

1250 Maryland Avenue

1250 MARYLAND AVENUE SW
WASHINGTON, DC 20024

BEYER BLINDER BELLE
3307 M Street Northwest, Suite 301
Washington, DC, 20007
202 333 8000

MECHANICAL & PLUMBING
HURST ENGINEERS
703-534-7872

ELECTRICAL
POWER DESIGN INC.
727-497-9811

STRUCTURAL
RATHGEBBER GOSS ASSOCIATES
301-590-0071

CIVIL
GORDON DC
202-869-1600

LANDSCAPE
OVS
202-546-7575

INTERIORS
KTGY SDDG
312-274-0707

LIGHTING
CM KLING + ASSOCIATES
703-684-6270

KEY PLAN

STAMP

NO	DATE	DESCRIPTION
4	6/6/25	ISSUED FOR CONSTRUCTION
A	01/23/25	PERMIT RESPONSE

REVISIONS

SUBMITTAL

ISSUED FOR CONSTRUCTION

DRAWING TITLE

SLAB EDGE - LEVEL 11 TO ROOF

SCALE	As indicated
DATE	05/16/25
PROJECT NUMBER	6415.00

DRAWING NUMBER

A058

of

Autodesk Docs://6415 - 1250 Maryland Avenue NW/6415-1250 Maryland Ave-R24.rvt

6/4/2025 6:18:23 PM