NOTE IF THIS SHEET IS NOT 36"W X 48"D THEN IT IS NOT THE INTENDED SIZE. IN ALL CASES, WORK TO FIGURED DIMENSIONS.

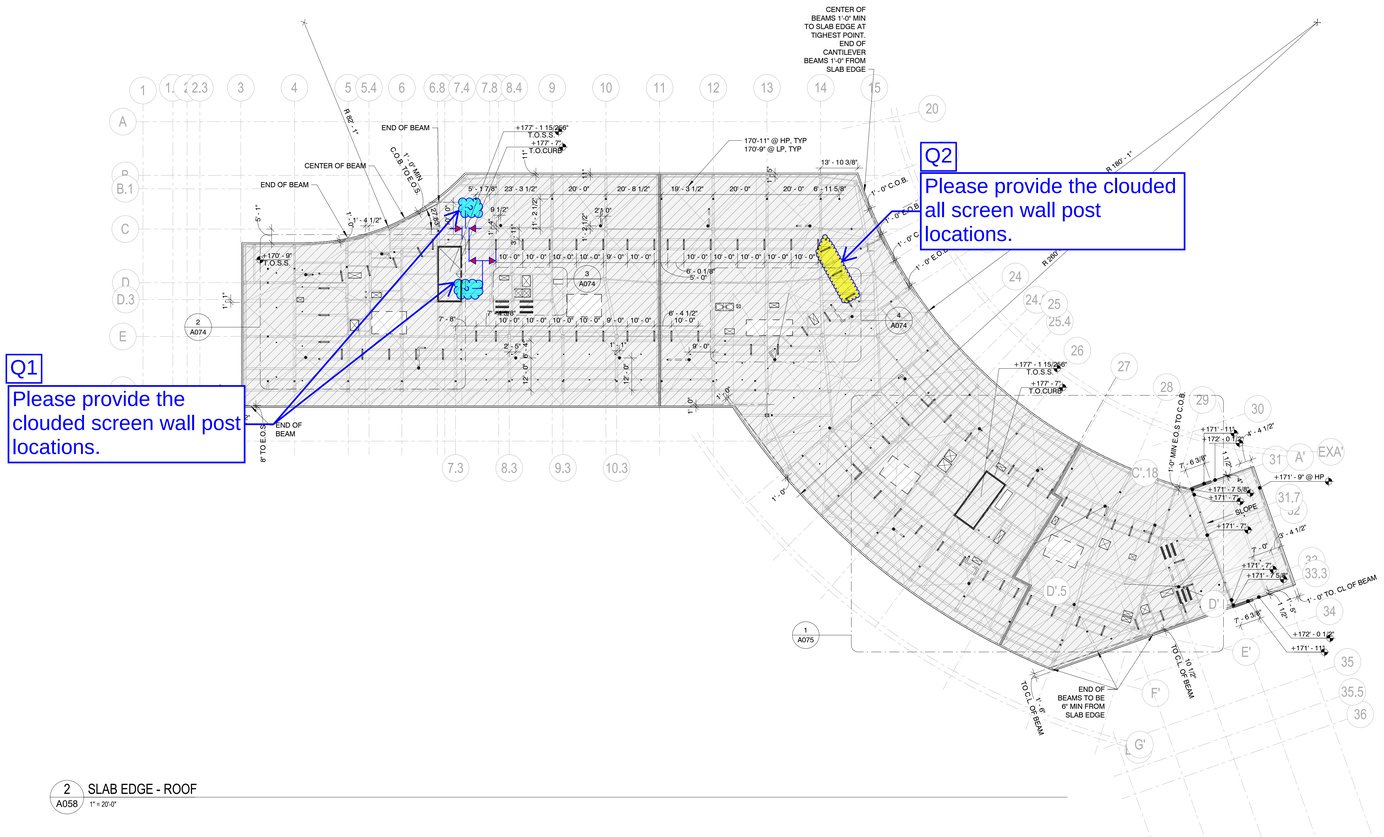

2 A058 SLAB EDGE - ROOF
1" = 20'-0"

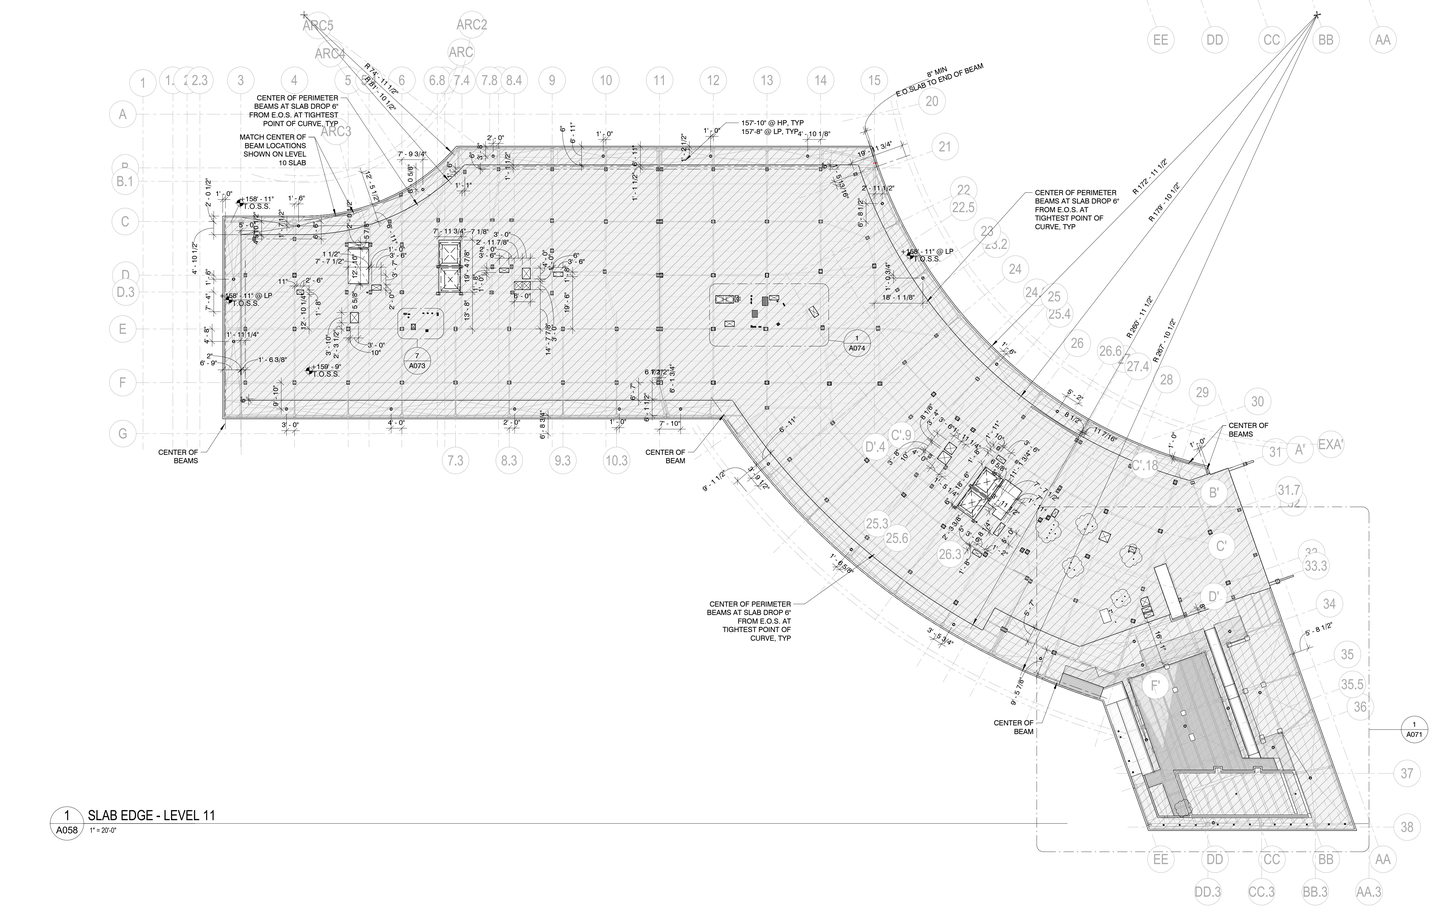

1 A058 SLAB EDGE - LEVEL 11
1" = 20'-0"

NEW FLOOR STEEL STRUCTURE NOTES:

1. SEE STRUCTURAL DRAWINGS FOR STEEL SIZING & LOCATIONS
2. NEW STEEL COLUMNS ALIGNED W/ EXISTING CONCRETE COLUMNS BELOW UNLESS NOTED OTHERWISE. DIMENSIONS PROVIDED FOR COLUMNS NOT ALIGNED W/ BELOW.
3. SEE STRUCTURAL DRAWINGS FOR STEEL COLUMN SIZING & SHAPE. RECTANGULAR GRAPHIC SHOWN IN ARCHITECTURAL PLANS ALSO REPRESENTS GYPSUM FURRING NEEDED FOR RATING.

LEGEND
- NEW STEEL COLUMN, ALIGNED WITH COLUMN BELOW
- NEW STEEL COLUMN SUPPORTED BY BEAM BELOW, SEE DIMENSIONS

SLAB EDGE DRAWING NOTES:

1. SLAB DRAWINGS ARE BASED ON ORIGINAL EXISTING DRAWINGS. ALL LOCATIONS VERIFIED I NOTIFY AR OPENINGS DRAWINGS INFILL.
2. SEE DEMO NEW OPEN DEMOLITIO ARE TO BE
3. SEE ADDIT DEMOLITIO ELEVATOR
4. NEW INFIL EXTENSIO ADJACENT NOTED OT
5. SEE A06# SERIES FOR ENLARGED PERIMETER PLANS. DIMENSIONS OF PERIMETER OMMITED FROM THIS

LEGEND
- EXISTING SLAB,

SK#15
2 pages
4 Queries
Date: 06-27-2025

0 5' 10' 20' 40'

DOB STAMP

1250 Maryland Avenue
1250 MARYLAND AVENUE SW
WASHINGTON, DC 20024

BEYER BLINDER BELLE
3307 M Street Northwest, Suite 301
Washington, DC, 20007
202 333 8000

MECHANICAL & PLUMBING
HURST ENGINEERS
703-534-7872

ELECTRICAL
POWER DESIGN INC.
727-497-9811

STRUCTURAL
RATHGEBBER GOSS ASSOCIATES
301-590-0071

CIVIL
GORDON DC
202-869-1600

LANDSCAPE
OVS
202-546-7575

INTERIORS
KTGY SDDG
312-274-0707

LIGHTING
CM KLING + ASSOCIATES
703-684-6270

KEY PLAN

STAMP

NO	DATE	DESCRIPTION
4	6/6/25	ISSUED FOR CONSTRUCTION
A	01/23/25	PERMIT RESPONSE

REVISIONS

SUBMITTAL

ISSUED FOR CONSTRUCTION

DRAWING TITLE

SLAB EDGE - LEVEL 11 TO ROOF

SCALE	As indicated
DATE	05/16/25
PROJECT NUMBER	6415.00

DRAWING NUMBER

A058

of

Autodesk Docs://6415 - 1250 Maryland Avenue SW/A415 - 1250 Maryland Ave-R24.rvt

6/4/2025 6:18:23 PM

NOTE IF THIS SHEET IS NOT 30"W x 42"D
THEN IT IS NOT THE INTENDED SIZE. IN ALL
CASES, WORK TO FIGURED DIMENSIONS.

0 0.5' 1' 2'

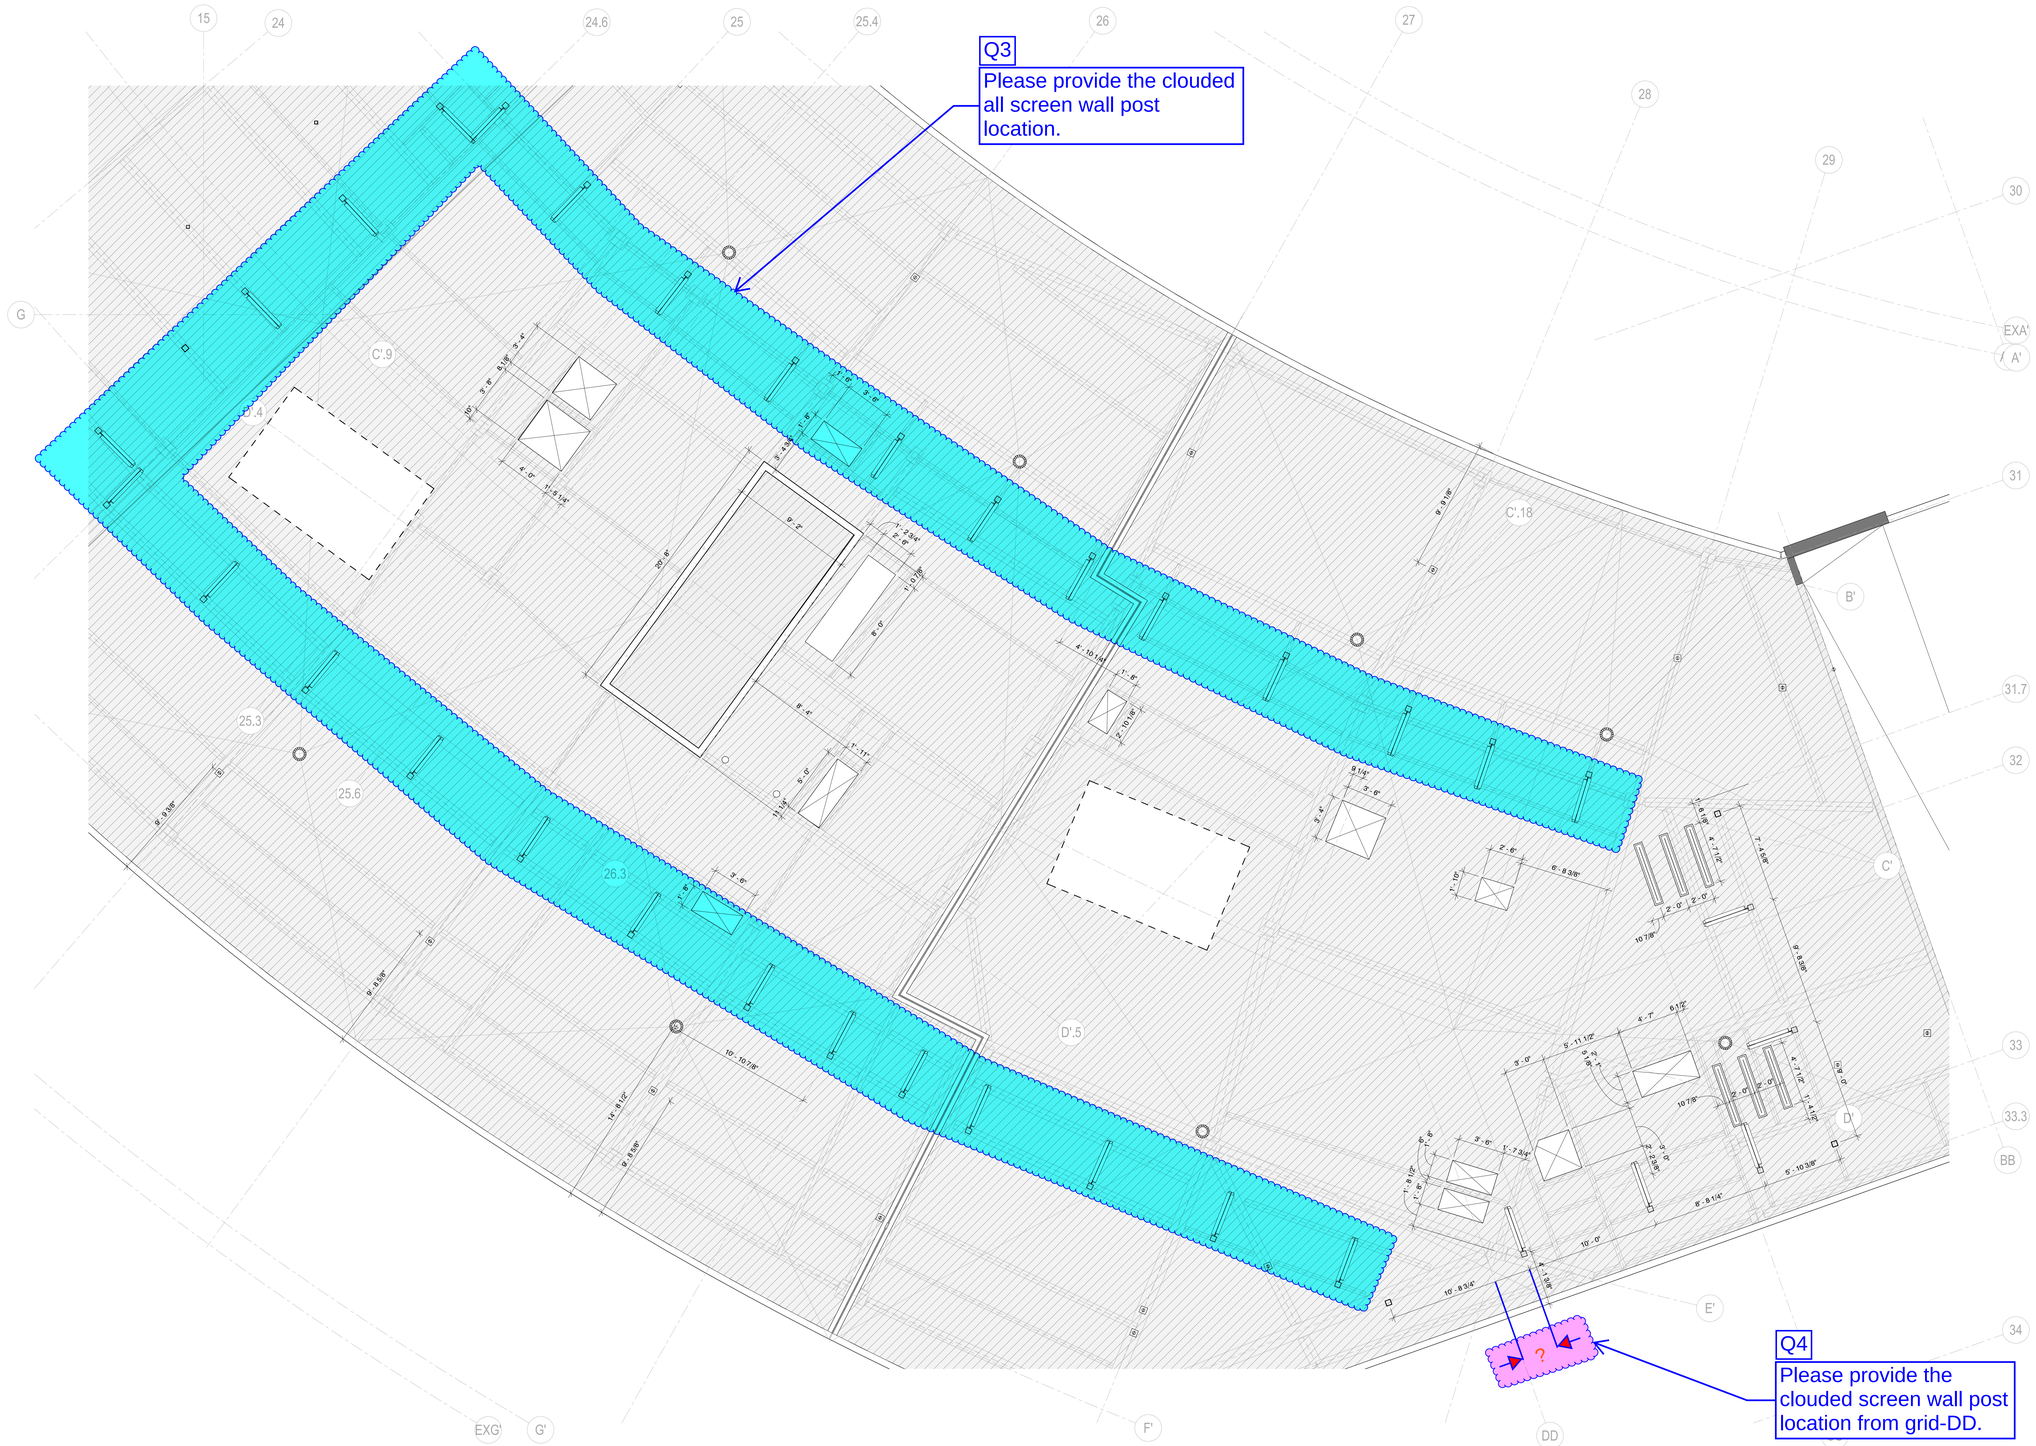

1 A075 SLAB EDGE - ROOF - Callout 4
1/4" = 1'-0"

DOB STAMP

1250 Maryland Avenue
1250 MARYLAND AVENUE SW
WASHINGTON, DC 20024

BEYER BLINDER BELLE
3307 M Street Northwest, Suite 301
Washington, DC, 20007
202 333 8000

MECHANICAL & PLUMBING
HURST ENGINEERS
703-534-7872

ELECTRICAL
POWER DESIGN INC.
727-497-9811

STRUCTURAL
RATHGEBER GOSS ASSOCIATES
301-590-0071

CIVIL
GORDON DC
202-869-1600

LANDSCAPE
OVS
202-546-7575

INTERIORS
KTGY SDDG
312-274-0707

LIGHTING
CM KLING + ASSOCIATES
703-684-6270

KEY PLAN

STAMP

NO	DATE	DESCRIPTION

REVISIONS

SUBMITTAL

ISSUED FOR CONSTRUCTION

DRAWING TITLE

ENLARGED SLAB EDGE PENETRATION PLANS

SCALE	1/4" = 1'-0"
DATE	05/16/25
PROJECT NUMBER	6415.00
DRAWING NUMBER	

A075

of

Autodesk Docs://6415 - 1250 Maryland Avenue/WX-6415-1250-Maryland-Avenue-R24.rvt

6/4/2025 5:18:58 PM