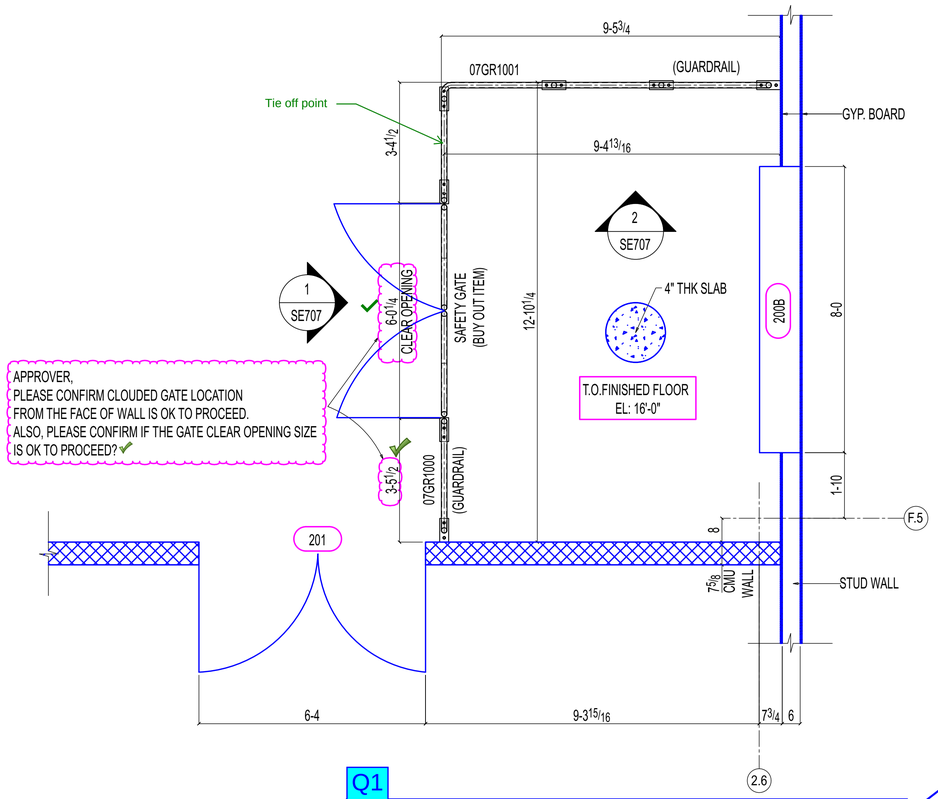

1 E703 MEZZA

NOTE:
1. ALL ELEVATION ARE
2. ALL GUARDRAILS AR

APPROVER,
WE HAVE FOLLOWED 1 1/2" SCH 40 PIPE FOR
THE FLOOR GUARDRAILS. PLEASE CONFIRM IF IT IS ACCEPTABLE.

Q1
Please advise on clouded field measurement if the survey dimension measured between outer face of the wall or the inner face of wall? since we have 1-0 + deviation comparing to arch dimensions.

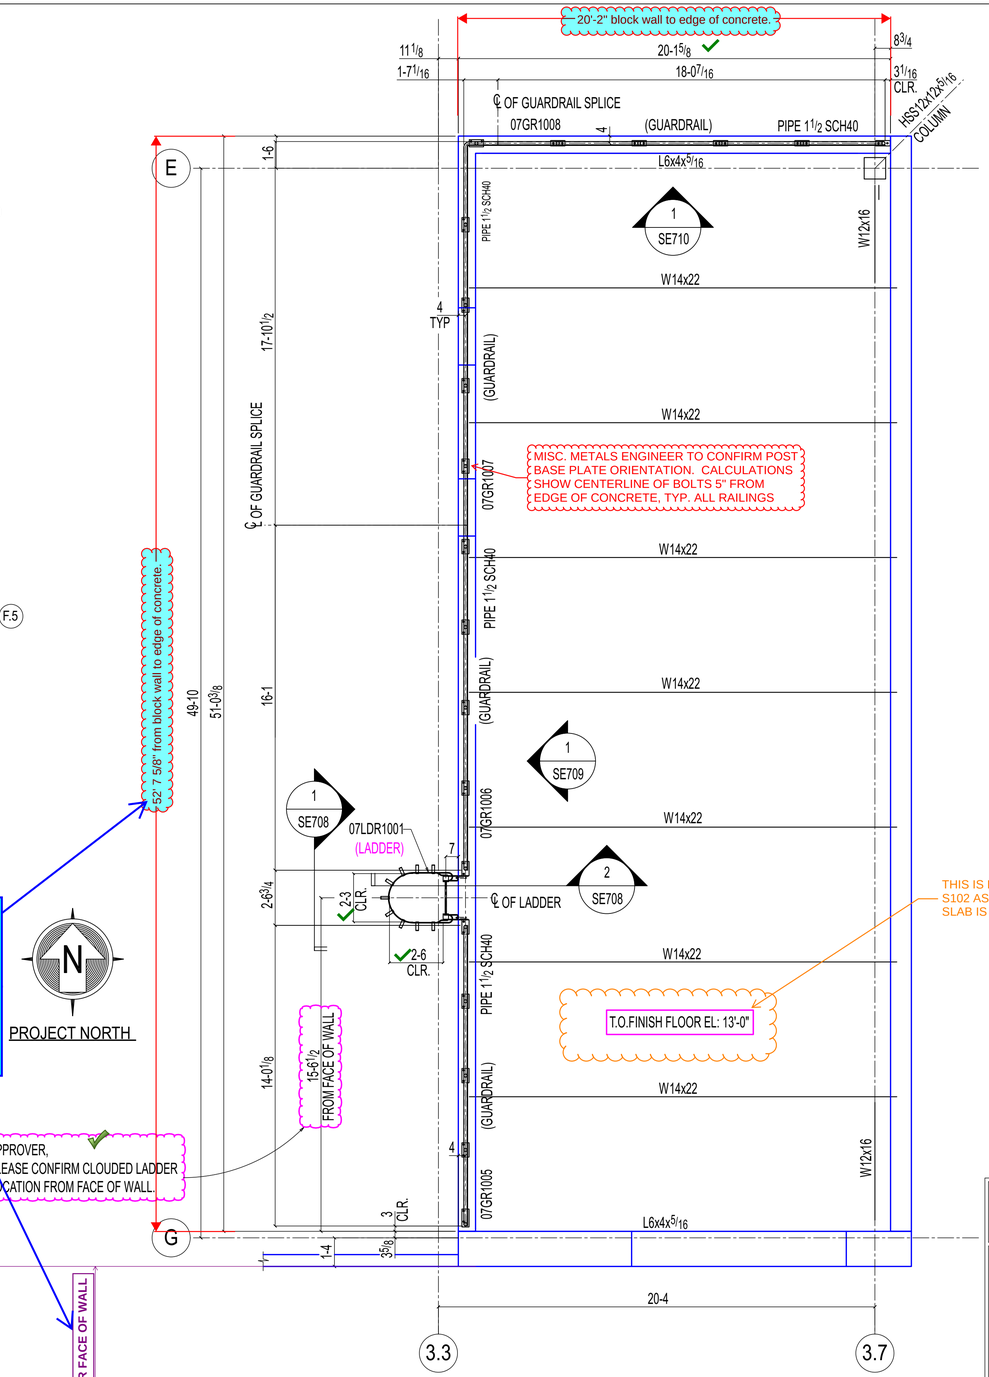

APPROVER,
PLEASE CONFIRM CLOUDED LADDER
LOCATION FROM FACE OF WALL.

2 E703 LUBE ROOM DUST CAP (LADDER AND GUARDRAIL PLAN)

(REF: 1/A102,5/A173)

NOTE:
1. ALL ELEVATION ARE REFERENCED FROM THE FINISHED FLOOR EL: [0'-0"] = DATUM EL: 100'-0" (U.N.O).
2. ALL GUARDRAILS ARE PIPE 1 1/2 SCH40 (U.N.O)

APPROVER,
WE HAVE FOLLOWED 1 1/2" SCH 40 PIPE FOR
THE FLOOR GUARDRAILS. PLEASE CONFIRM IF IT IS ACCEPTABLE.

TRUE NORTH

PROJECT NORTH

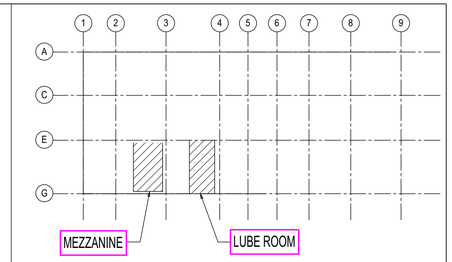

KEY PLAN

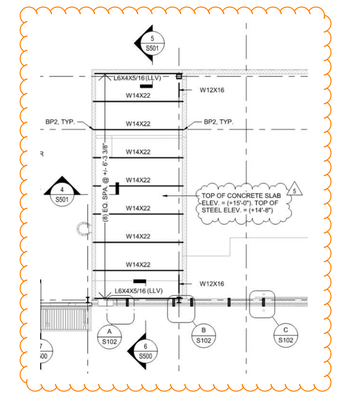

THIS IS INCORECT. REFER TO SHEET
S102 AS THE TOP OF CONCRETE
SLAB IS SHOWN AS +15'-0" AFF

REVISIONS

REV#	DWN BY	DESCRIPTION	DATE
A	SRP	ISSUED FOR APPROVAL	Jun 16 2025

THE INFORMATION NOTED HEREON THIS DRAWING IS THE
PROPERTY OF STEEL FAB ENTERPRISES, INC. AND SHALL
NOTED BE USED WITHOUT WRITTEN CONSENT.

STEEL FAB
ENTERPRISES, LLC
AISC CERTIFIED FABRICATOR AND ERECTOR
MISCELLANEOUS METALS FABRICATOR AND ERECTORS
623 BAUMGARDNER ROAD, LANCASTER, PA 17603
TEL. (717)464-0330 FAX (717)464-9464
WWW.STEELFABENTERPRISES.COM

PROJECT OWNER : CK CAPITAL, LLC
PROJECT DESCRIPTION : CLEVELAND BROTHERS-MILESBURG
PROJECT ADDRESS : 4025N. EAGLE VALLEY ROAD, HOWARD, PA 16841
CONTRACTOR : KINSLEY CONSTRUCTION, INC.

DRAWN BY : BAS	DATE : 5-20-25	PROJ. NO. : 25912	REV # A
CHECKED BY : SRP	DATE : 5-20-25	DWG NO. : E703	

DWG DESCRIPTION : GUARDRAIL & LADDER PLAN

SK#19
12-09-2025

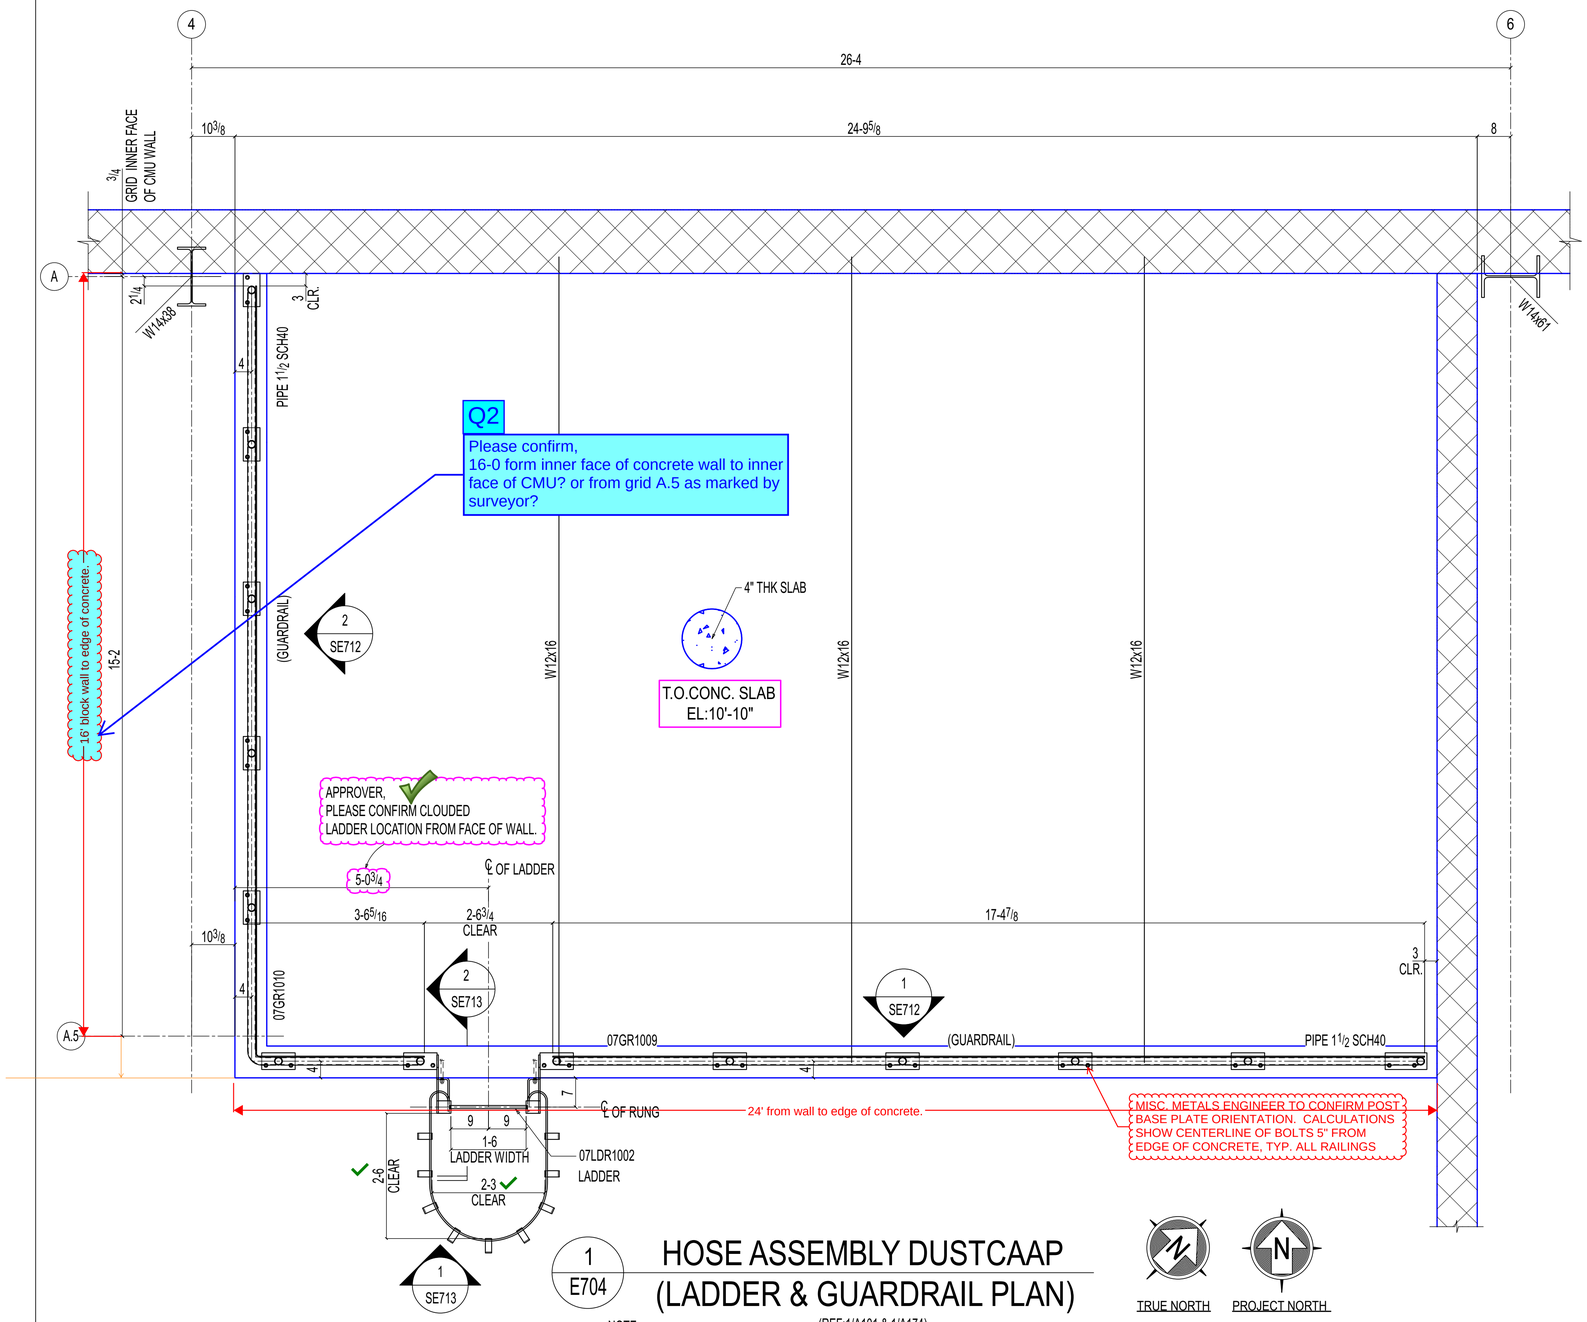

1 E704 HOSE ASSEMBLY DUSTCAAP (LADDER & GUARDRAIL PLAN)

(REF:1/A101 & 1/A174)

TRUE NORTH PROJECT NORTH

NOTE:
1. ALL ELEVATION ARE REFERENCED FROM THE FINISHED FLOOR EL: [0'-0"] = DATUM EL:100'-0" (U.N.O).
2. ALL GUARDRAILS ARE PIPE 1 1/2 SCH40 (U.N.O).

APPROVER,
WE HAVE FOLLOWED 1 1/2" SCH 40 PIPE FOR THE FLOOR GUARDRAILS.PLEASE CONFIRM IF IT IS IT OK TO PROCEED?

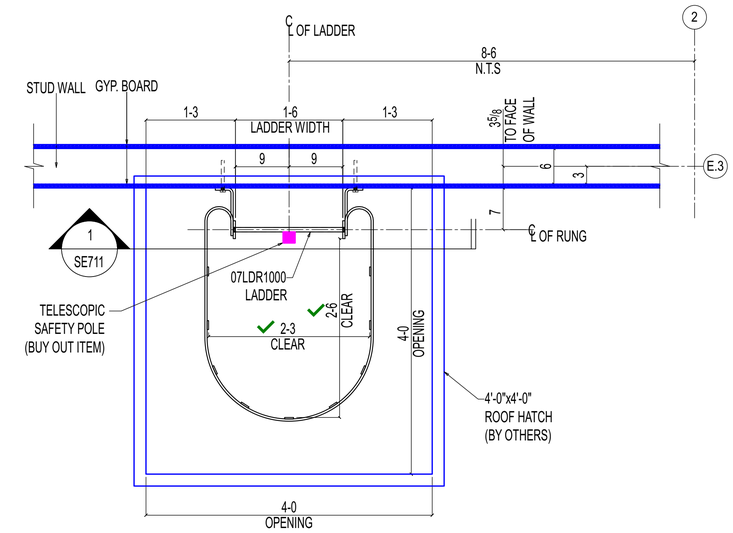

2 E704 MEZZANINE ROOF ACCESS LADDER

(REF:1/A102 & 3/S411)

TRUE NORTH PROJECT NORTH

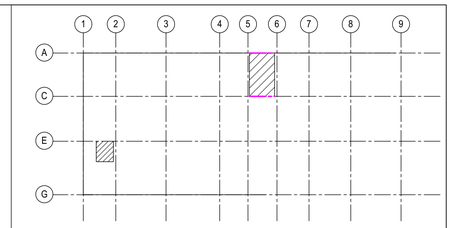

KEY PLAN

REVISIONS

REV#	DWN BY	DESCRIPTION	DATE
A	SRP	ISSUED FOR APPROVAL	Jun 16 2025

THE INFORMATION NOTED HEREON THIS DRAWING IS THE PROPERTY OF STEEL FAB ENTERPRISES, INC. AND SHALL NOTED BE USED WITHOUT WRITTEN CONSENT.

STEEL FAB ENTERPRISES, LLC
AISC CERTIFIED FABRICATOR AND ERECTOR
MISCELLANEOUS METALS FABRICATOR AND ERECTORS
623 BAUMGARDNER ROAD, LANCASTER, PA 17603
TEL. (717)464-0330 FAX (717)464-9464
WWW.STEELFABENTERPRISES.COM

PROJECT OWNER : CK CAPITAL, LLC
PROJECT DESCRIPTION : CLEVELAND BROTHERS-MILESBURG
PROJECT ADDRESS : 4025N. EAGLE VALLEY ROAD, HOWARD, PA 16841
CONTRACTOR : KINSLEY CONSTRUCTION, INC.

DRAWN BY : BAS	DATE : 5-20-25	PROJ. NO. : 25012	REV # A
CHECKED BY : SRP	DATE : 5-20-25	DWG NO. : E704	

DWG DESCRIPTION : HOSE ASSEMBLY DUSTCAAP (LADDER & HUARDRAIL PLAN)

Gate has not been released for fabrication. What is holding this up? We need to get gate columns to GC to be embedded.

Q3

We need responde for SK#17-Q10 to proceed further.
Please see the attached SK#17 in this mail.

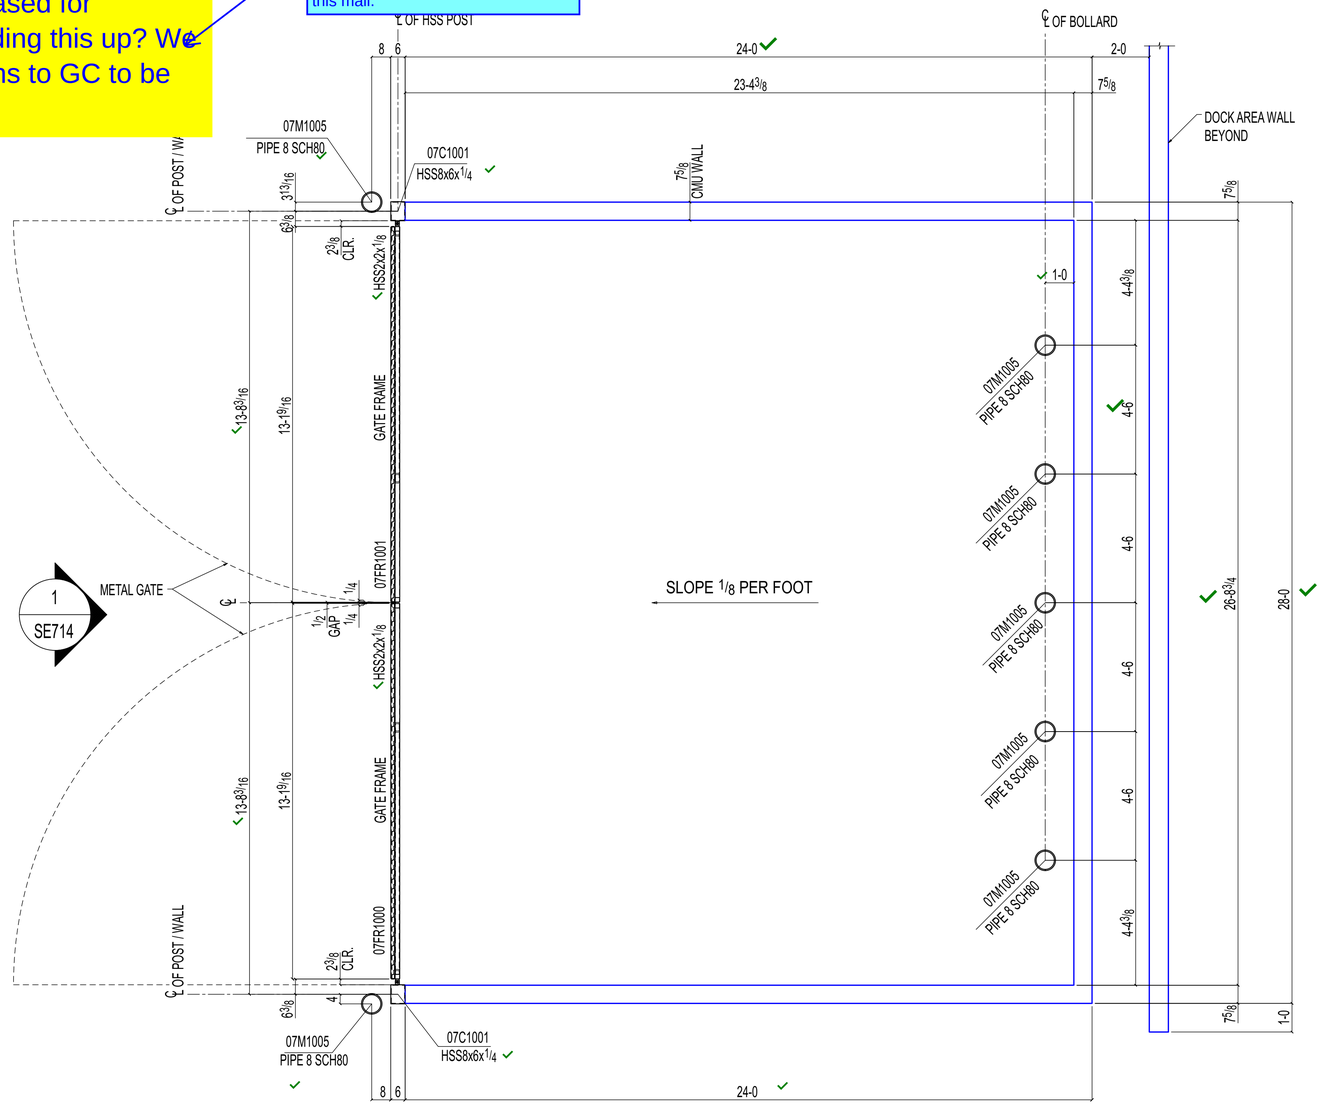

1
E705

REFUSE CONTAINER ENCLOSURE
GATE FRAMING PLAN

(REF: 1/A182)

TRUE NORTH

PROJECT NORTH

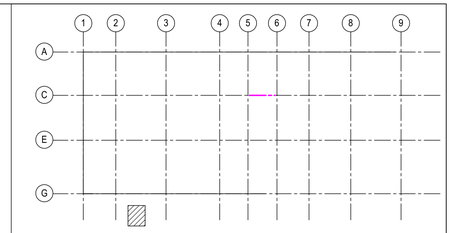

KEY PLAN

REVISIONS

REV#	DWN BY	DESCRIPTION	DATE
A	SRP	ISSUED FOR APPROVAL	Jun 16 2025

THE INFORMATION NOTED HEREON THIS DRAWING IS THE PROPERTY OF STEEL FAB ENTERPRISES, INC. AND SHALL NOTED BE USED WITHOUT WRITTEN CONSENT.

STEEL FAB
ENTERPRISES, LLC
AISC CERTIFIED FABRICATOR AND ERECTOR
MISCELLANEOUS METALS FABRICATOR AND ERECTORS
623 BAUMGARDNER ROAD, LANCASTER, PA 17603
TEL. (717)464-0330 FAX (717)464-9464
WWW.STEELFABENTERPRISES.COM

PROJECT OWNER : CK CAPITAL, LLC

PROJECT DESCRIPTION : CLEVELAND BROTHERS-MILESBURG

PROJECT ADDRESS : 1025N. EAGLE VALLEY ROAD, HOWARD, PA 16841

CONTRACTOR : KINSLEY CONSTRUCTION, INC.

DRAWN BY : BAS	DATE : 5-20-25	PROJ. NO. : 25912	REV # A
CHECKED BY : SRP	DATE : 5-20-25	DWG NO. : E705	

DWG DESCRIPTION : REFUSE CONTAINER ENCLOSURE FRAMING PLAN

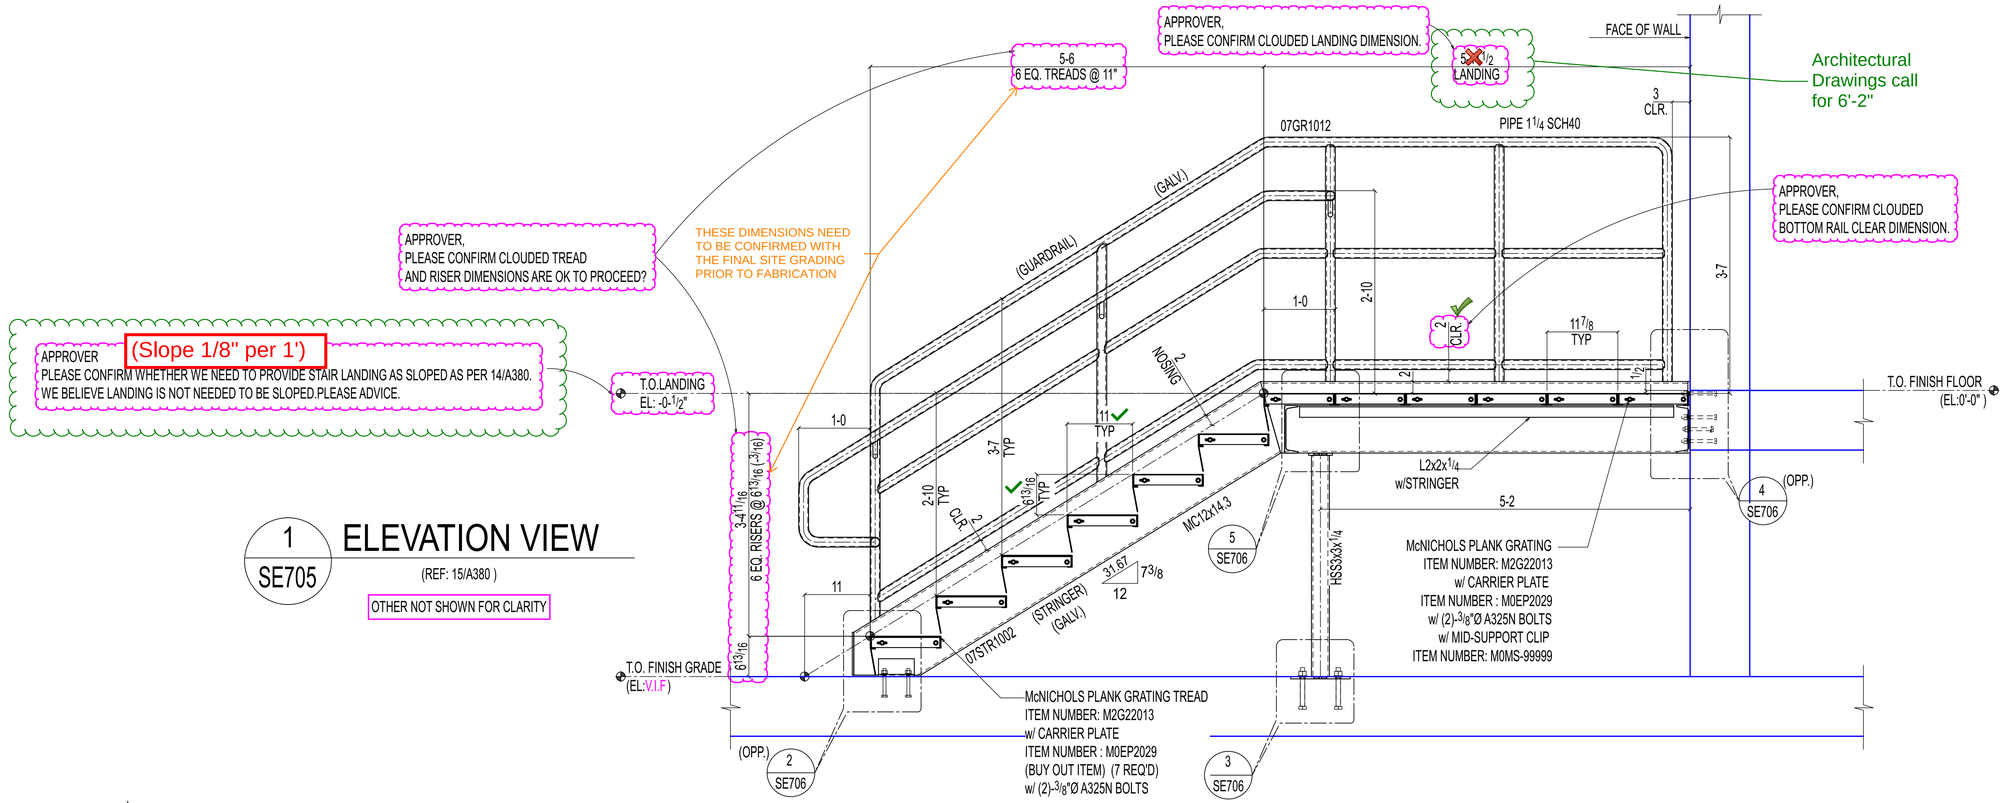

1 / SE705 **ELEVATION VIEW**

(REF: 15/A380)

OTHER NOT SHOWN FOR CLARITY

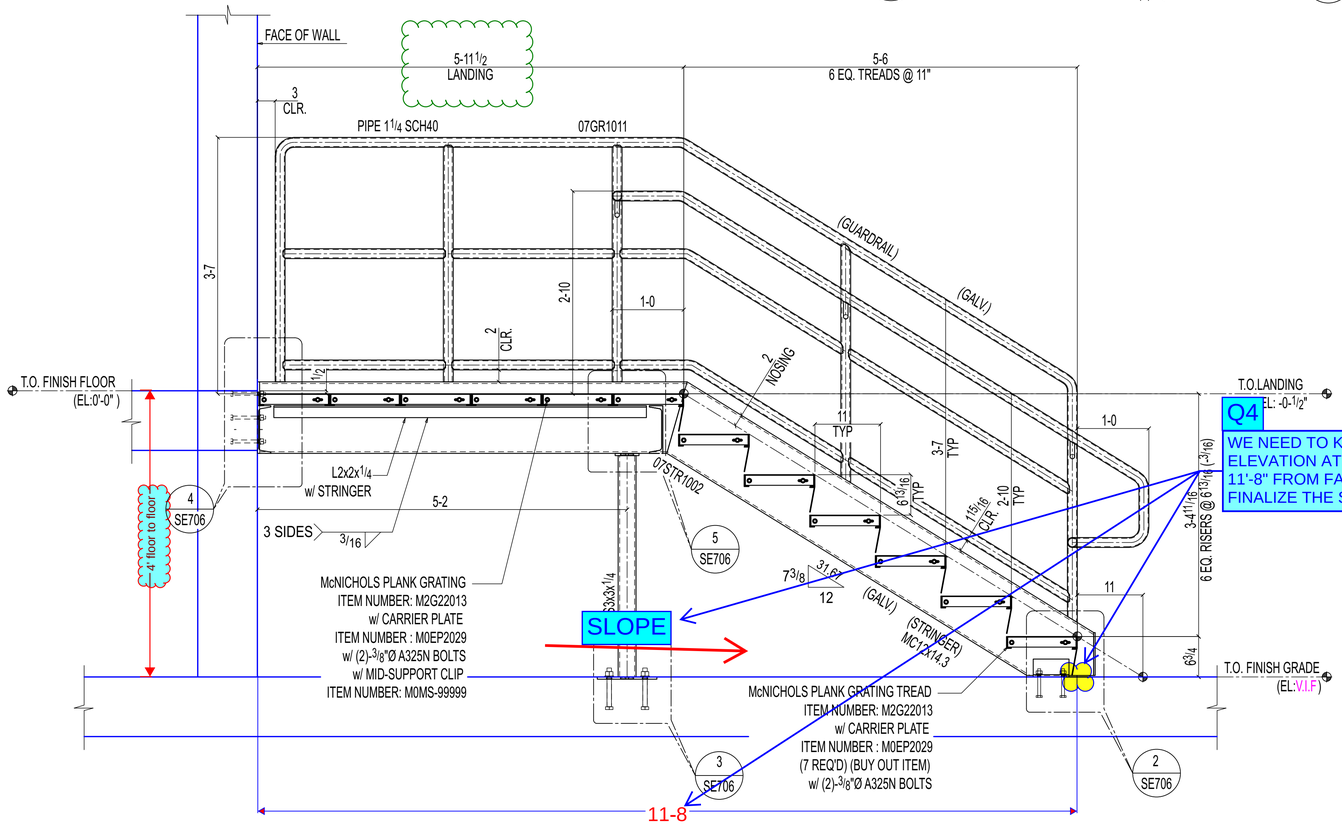

2 / SE705 **ELEVATION VIEW**

(REF: 15/A380)

OTHER NOT SHOWN FOR CLARITY

ERECTOR NOTE:
1. WIRE BRUSH GALVANIZED SURFACE AS REQUIRED FOR WELDING.
2. TOUCHUP ALL FIELD WELDS WITH ZINC RICH PAINT (U.N.O)

REVISIONS

REV#	DWN BY	DESCRIPTION	DATE
A	SRP	ISSUED FOR APPROVAL	Jun 16 2025

THE INFORMATION NOTED HEREON THIS DRAWING IS THE PROPERTY OF STEEL FAB ENTERPRISES, INC. AND SHALL NOTED BE USED WITHOUT WRITTEN CONSENT.

STEEL FAB ENTERPRISES, LLC
AISC CERTIFIED FABRICATOR AND ERECTOR
MISCELLANEOUS METALS FABRICATOR AND ERECTORS
623 BAUMGARDNER ROAD, LANCASTER, PA 17603
TEL. (717)464-0330 FAX (717)464-9464
WWW.STEELFABENTERPRISES.COM

PROJECT OWNER : CK CAPITAL, LLC

PROJECT DESCRIPTION : CLEVELAND BROTHERS-MILESBURG

PROJECT ADDRESS : 1025N. EAGLE VALLEY ROAD, HOWARD, PA 16841

CONTRACTOR : KINSLEY CONSTRUCTION, INC.

DRAWN BY : BAS	DATE : 5-20-25	PROJ. NO. : 25012	REV # A
CHECKED BY : SRP	DATE : 5-20-25	DWG NO. : SE705	

DWG DESCRIPTION : STAIR ELEVATION VIEW

APPROVER,
PLEASE CONFIRM CLOUDED STAR LOCATION (CHANNEL OUTER END)
FROM DOOR OPENING IS OK TO PROCEED?

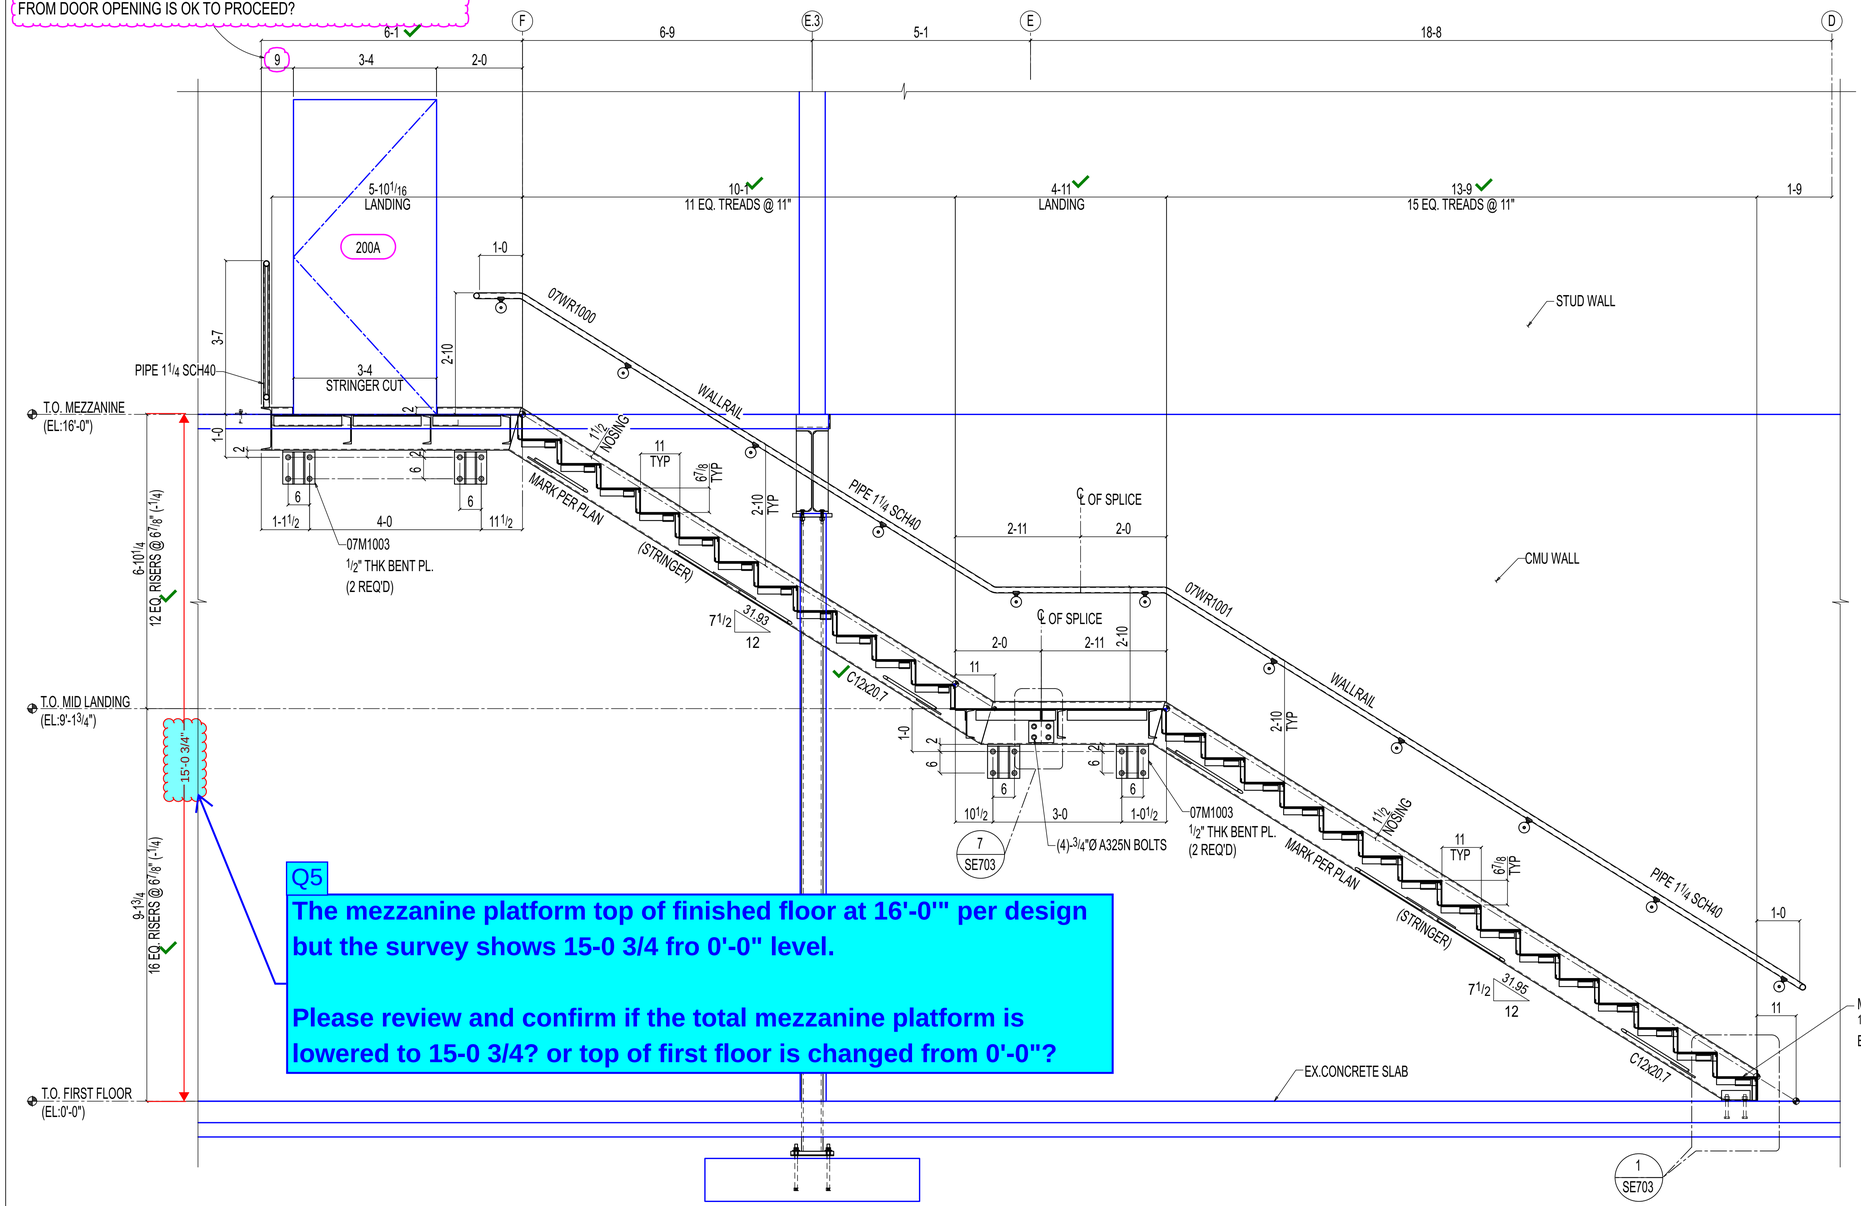

Q5

The mezzanine platform top of finished floor at 16'-0'" per design but the survey shows 15-0 3/4 fro 0'-0" level.

Please review and confirm if the total mezzanine platform is lowered to 15-0 3/4? or top of first floor is changed from 0'-0"?

1 SE701 ELEVATION VIEW

(REF: 2/A380)

OTHER NOT SHOWN FOR CLARITY

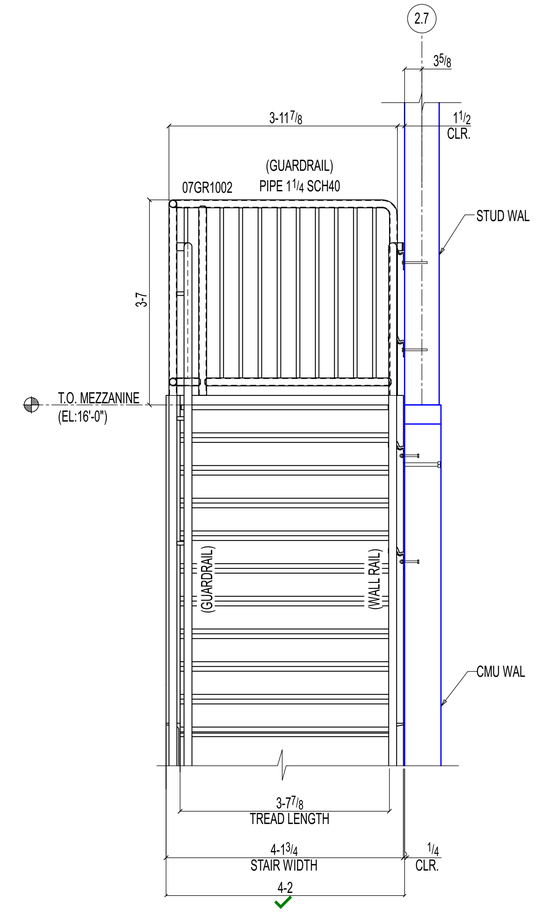

2 SE701 ELEVATION VIEW

(REF: 4/A380)

OTHER NOT SHOWN FOR CLARITY

REVISIONS

REV#	DWN BY	DESCRIPTION	DATE
A	SRP	ISSUED FOR APPROVAL	Jun 16 2025

THE INFORMATION NOTED HEREON THIS DRAWING IS THE PROPERTY OF STEEL FAB ENTERPRISES, INC. AND SHALL NOTED BE USED WITHOUT WRITTEN CONSENT.

STEEL FAB
ENTERPRISES, LLC
AISC CERTIFIED FABRICATOR AND ERECTOR
MISCELLANEOUS METALS FABRICATOR AND ERECTORS
623 BAUMGARDNER ROAD, LANCASTER, PA 17603
TEL. (717)464-0330 FAX (717)464-9464
WWW.STEELFABENTERPRISES.COM

PROJECT OWNER : CK CAPITAL, LLC

PROJECT DESCRIPTION : CLEVELAND BROTHERS-MILESBURG

PROJECT ADDRESS : 1025N. EAGLE VALLEY ROAD, HOWARD, PA 16841

CONTRACTOR : KINSLEY CONSTRUCTION, INC.

DRAWN BY : BAS	DATE : 5-20-25	PROJ. NO. : 25012	REV # A
CHECKED BY : SRP	DATE : 5-20-25	DWG NO. : SE701	

DWG DESCRIPTION : ELEVATION VIEW

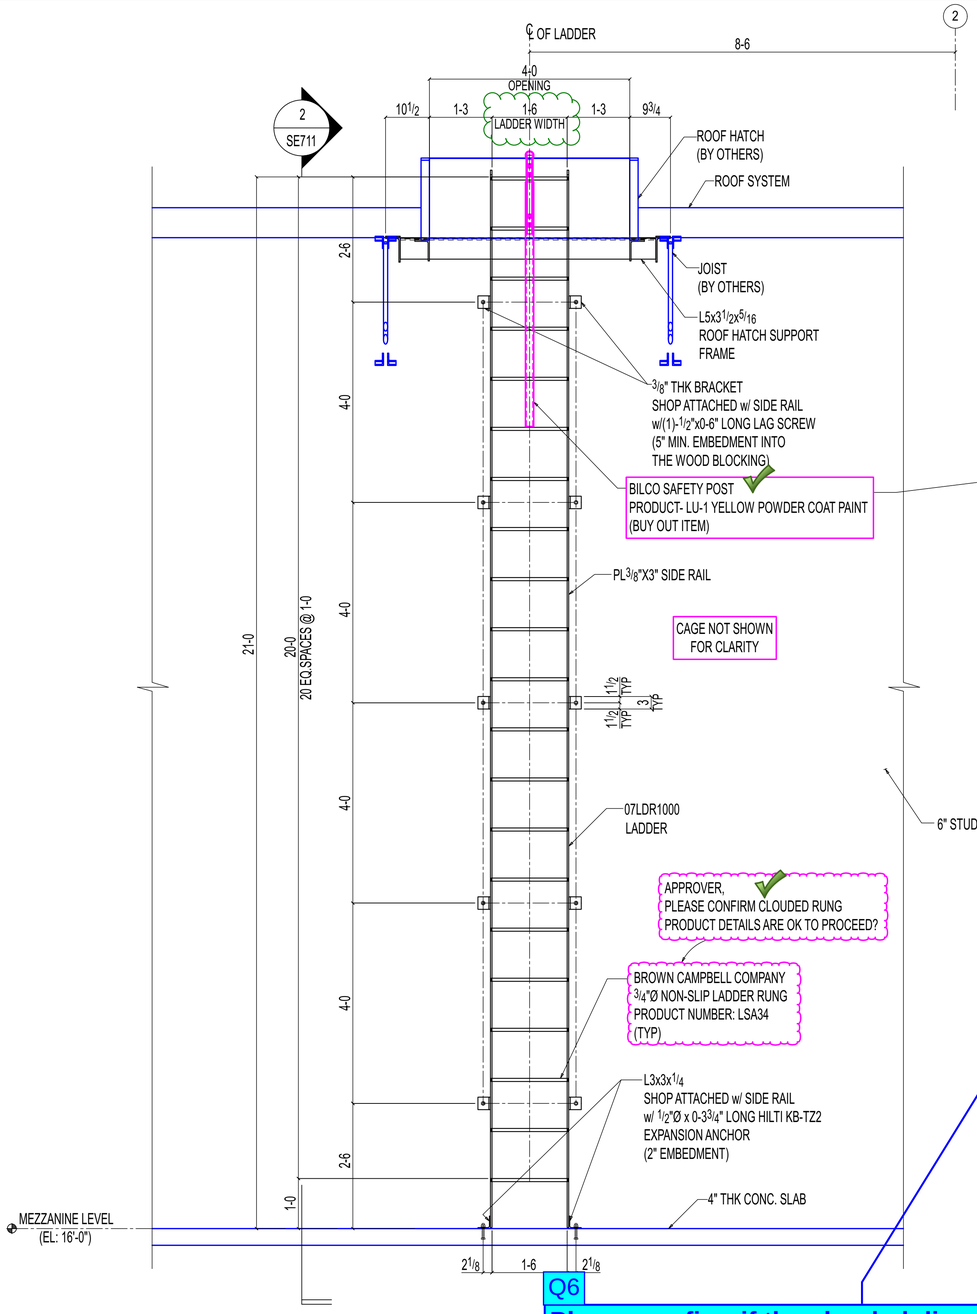

1 SE711 ELEVA

(R

OTHER NO

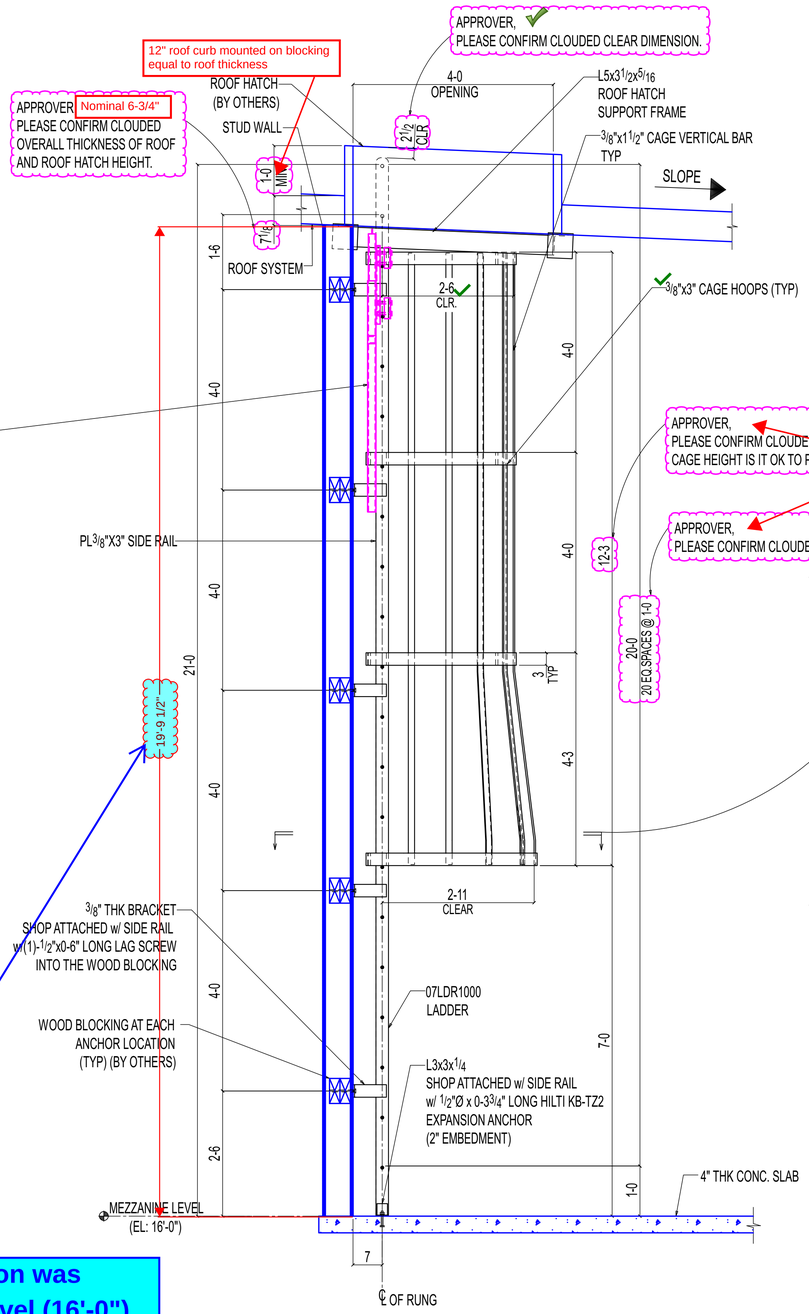

2 SE711 ELEVATION VIEW

(REF:3/A411)

OTHER NOT SHOWN FOR CLARITY

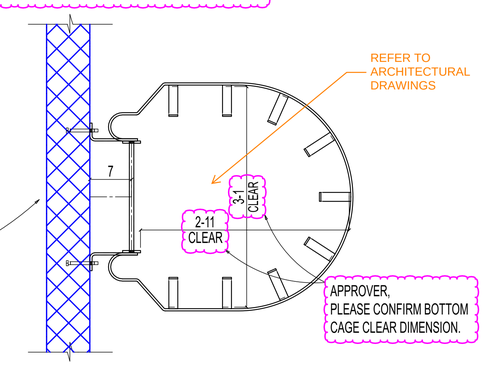

Q6

Please confirm if the clouded dimension was taken from the top of the mezzanine level (16'-0") since per the previous question Q5, it seems mezzanine finished floor may changed 15-0 3/4 from 16-0.

Please advise.

1. ALL ELEVATION ARE REFERENCED FROM THE FINISHED FLOOR EL: [0'-0"] = DATUM EL:100'-0" (U.N.O).

REVISIONS

REV#	DWN BY	DESCRIPTION	DATE
A	SRP	ISSUED FOR APPROVAL	Jun 16 2025

THE INFORMATION NOTED HEREON THIS DRAWING IS THE PROPERTY OF STEEL FAB ENTERPRISES, INC. AND SHALL NOT BE USED WITHOUT WRITTEN CONSENT.

STEEL FAB
ENTERPRISES, LLC
AISC CERTIFIED FABRICATOR AND ERECTOR
MISCELLANEOUS METALS FABRICATOR AND ERECTORS
623 BAUMGARDNER ROAD, LANCASTER, PA 17603
TEL. (717)464-0330 FAX (717)464-9464
WWW.STEELFABENTERPRISES.COM

PROJECT OWNER : CK CAPITAL, LLC

PROJECT DESCRIPTION : CLEVELAND BROTHERS-MILESBURG

PROJECT ADDRESS : 1025N. EAGLE VALLEY ROAD, HOWARD, PA 16841

CONTRACTOR : KINSLEY CONSTRUCTION, INC.

DRAWN BY : BAS	DATE : 5-20-25	PROJ. NO. : 25012	REV # A
CHECKED BY : SRP	DATE : 5-20-25	DWG NO. : SE711	

DWG DESCRIPTION : LADDER ELEVATION VIEW

THIS ELEVATION IS INCORRECT, REFER TO STR. DRAWINGS.

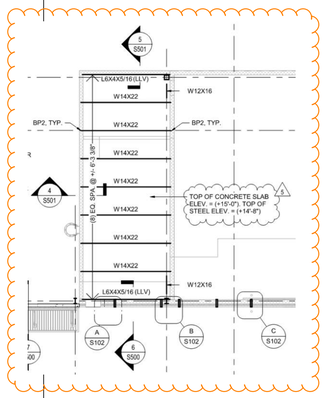

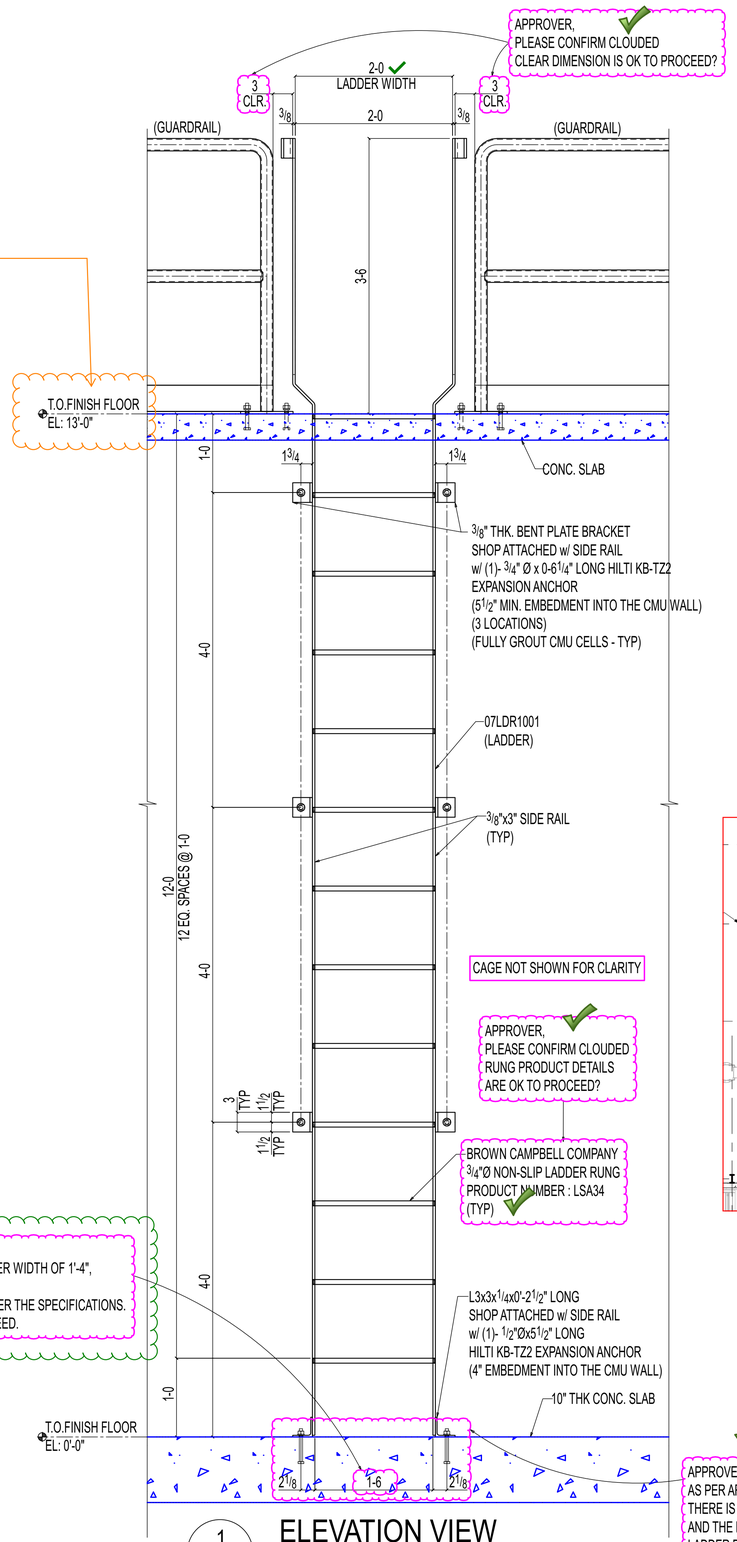

1 SE708 ELEVATION VIEW

OTHER NOT SHOWN FOR CLARITY

APPROVER, AS PER ARCHITECTURAL DRAWING 6/A101, THERE IS A CLEARANCE BETWEEN THE FLOOR AND THE LADDER. WE INTEND TO CONNECT THE LADDER DIRECTLY TO THE FLOOR INSTEAD. PLEASE CONFIRM IF THIS IS ACCEPTABLE TO PROCEED.

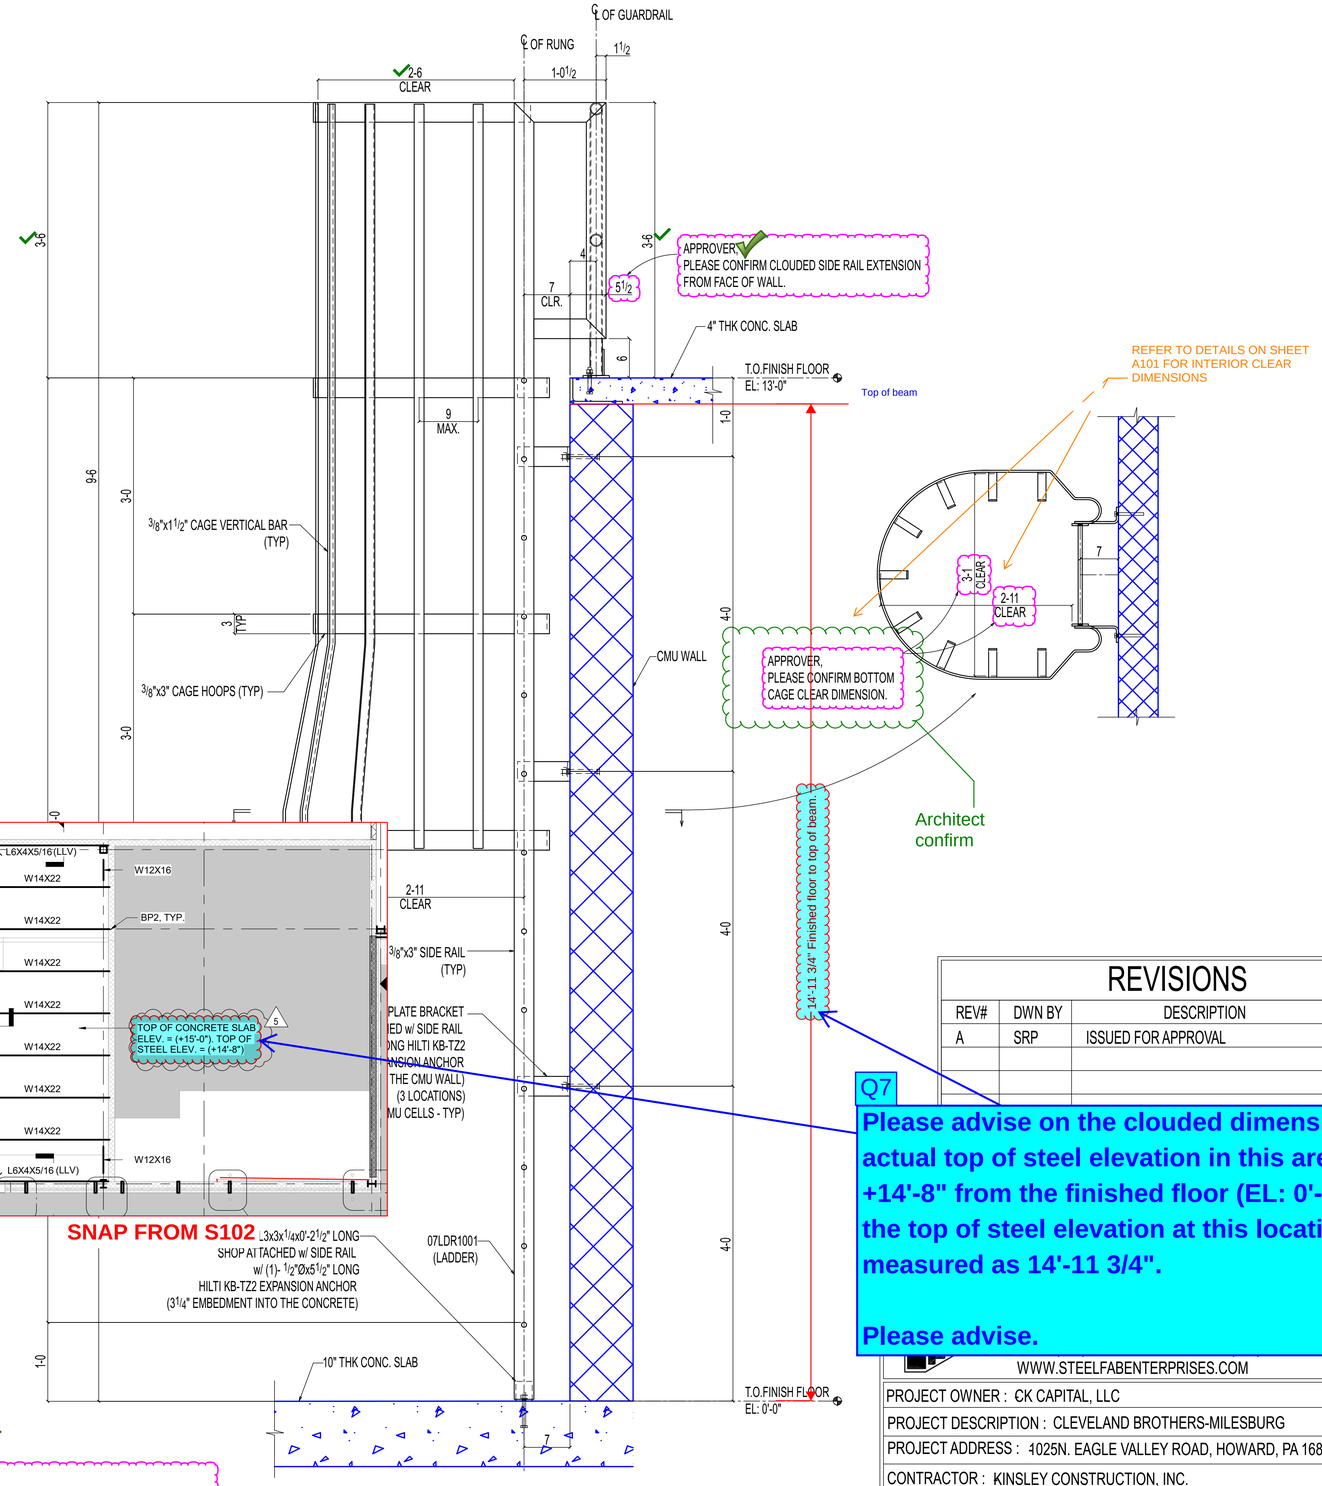

2 SE708 ELEVATION VIEW

OTHER NOT SHOWN FOR CLARITY

REVISIONS

REV#	DWN BY	DESCRIPTION	DATE
A	SRP	ISSUED FOR APPROVAL	Jun 16 2025

Q7

Please advise on the clouded dimension. The actual top of steel elevation in this area is +14'-8" from the finished floor (EL: 0'-0"), but the top of steel elevation at this location measured as 14'-11 3/4".

Please advise.

WWW.STEELFABENTERPRISES.COM

PROJECT OWNER : CK CAPITAL, LLC			
PROJECT DESCRIPTION : CLEVELAND BROTHERS-MILESBURG			
PROJECT ADDRESS : 4025N. EAGLE VALLEY ROAD, HOWARD, PA 16841			
CONTRACTOR : KINSLEY CONSTRUCTION, INC.			
DRAWN BY : BAS	DATE : 5-20-25	PROJ. NO. : 25012	REV # A
CHECKED BY : SRP	DATE : 5-20-25	DWG NO. : SE708	
DWG DESCRIPTION : LADDER ELEVATION VIEW			

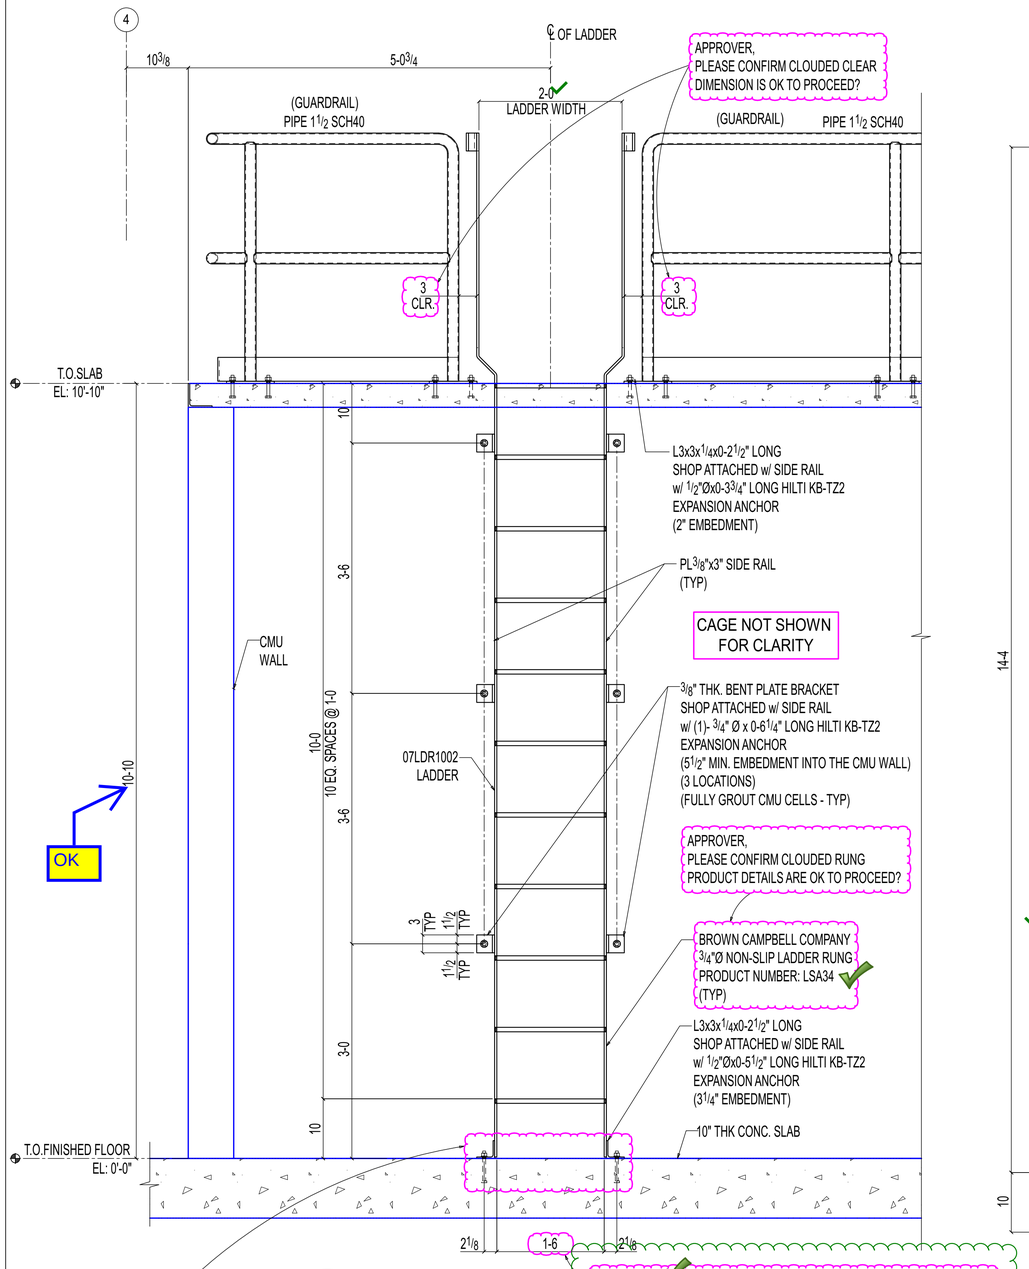

1 SE713 ELEVATION

OTHERS NOT SHOWN FOR CLARITY

APPROVER,
ARCHITECTURAL DRAWING 6/A101 INDICATES LADDER WIDTH OF 1'-4",
BUT THE SPECIFICATION SHOWS A WIDTH OF 1'-6".
WE HAVE FOLLOWED THE 1'-6" LADDER WIDTH AS PER THE SPECIFICATIONS.
PLEASE CONFIRM IF THIS IS ACCEPTABLE TO PROCEED.

APPROVER,
AS PER ARCHITECTURAL DRAWING 6/A101, THERE IS A CLEARANCE BETWEEN
THE FLOOR AND THE LADDER. WE INTEND TO CONNECT THE LADDER DIRECTLY
TO THE FLOOR INSTEAD. PLEASE CONFIRM IF THIS IS ACCEPTABLE TO PROCEED.

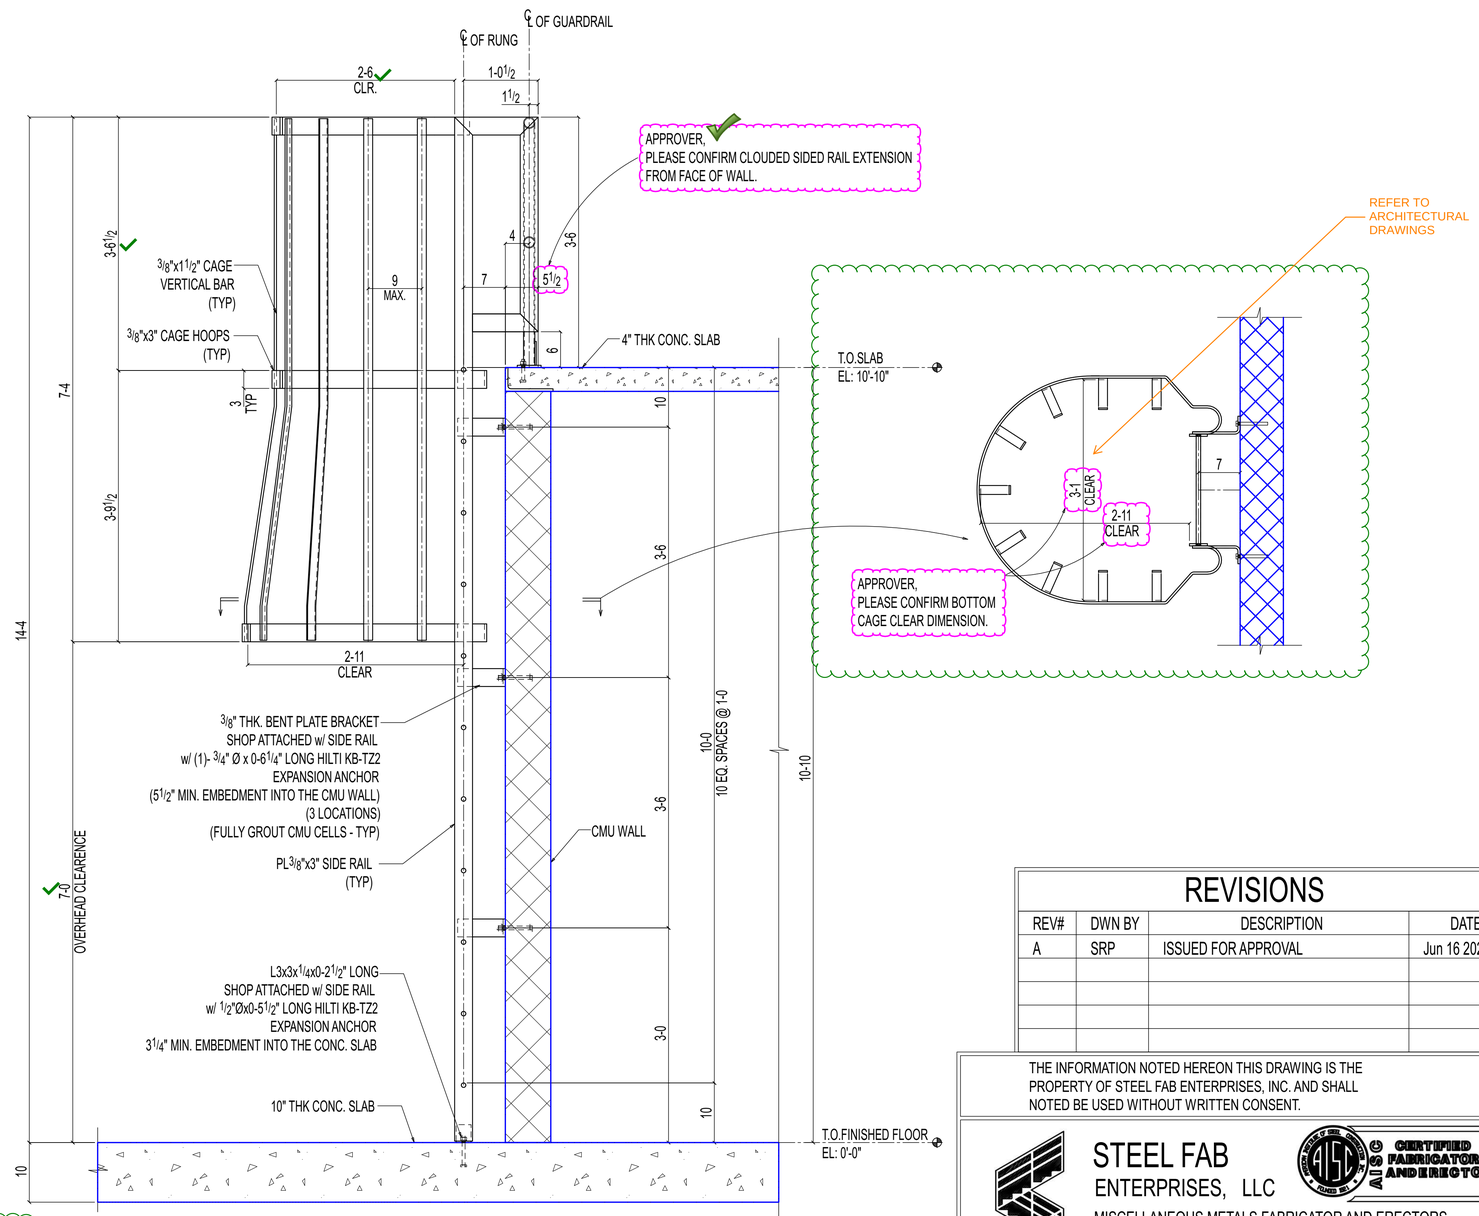

2 SE713 SECTION

(REF: 3/A411)

OTHERS NOT SHOWN FOR CLARITY

REVISIONS

REV#	DWN BY	DESCRIPTION	DATE
A	SRP	ISSUED FOR APPROVAL	Jun 16 2025

THE INFORMATION NOTED HEREON THIS DRAWING IS THE
PROPERTY OF STEEL FAB ENTERPRISES, INC. AND SHALL
NOTED BE USED WITHOUT WRITTEN CONSENT.

STEEL FAB
ENTERPRISES, LLC
AISC CERTIFIED FABRICATOR AND ERECTOR
MISCELLANEOUS METALS FABRICATOR AND ERECTORS
623 BAUMGARDNER ROAD, LANCASTER, PA 17603
TEL. (717)464-0330 FAX (717)464-9464
WWW.STEELFABENTERPRISES.COM

PROJECT OWNER : CK CAPITAL, LLC

PROJECT DESCRIPTION : CLEVELAND BROTHERS-MILESBURG

PROJECT ADDRESS : 1025N. EAGLE VALLEY ROAD, HOWARD, PA 16841

CONTRACTOR : KINSLEY CONSTRUCTION, INC.

DRAWN BY : BAS	DATE : 5-20-25	PROJ. NO. : 25012	REV # A
CHECKED BY : SRP	DATE : 5-20-25	DWG NO. : SE713	

DWG DESCRIPTION : LADDER ELEVATION VIEW